

Nr	Y	X	H	Kodi	Përkrimi	Burimi
19	7510638.742	4693478.994	648.212	40	Shtëpi-Ndertesë	PM
20	7510631.890	4693475.006	648.248	40	Shtëpi-Ndertesë	PM
36	7510641.829	4693478.618	648.248	40	Shtëpi-Ndertesë	PM
37	7510639.703	4693477.364	648.248	40	Shtëpi-Ndertesë	PM
38	7510639.232	4693465.791	648.248	40	Shtëpi-Ndertesë	PM
39	7510638.001	4693465.065	648.248	40	Shtëpi-Ndertesë	PM
40	7510632.905	4693473.355	648.248	40	Shtëpi-Ndertesë	PM
97	7510639.271	4693465.727	648.248	40	Shtëpi-Ndertesë	PM
98	7510641.077	4693466.793	648.248	40	Shtëpi-Ndertesë	PM
99	7510641.038	4693466.857	648.248	40	Shtëpi-Ndertesë	PM
100	7510645.005	4693469.197	648.248	40	Shtëpi-Ndertesë	PM
101	7510644.645	4693469.782	648.248	40	Shtëpi-Ndertesë	PM
102	7510646.463	4693470.855	648.248	40	Shtëpi-Ndertesë	PM



 Republika e Kosovës  
Qeveria -Vlada  
*Ministria e Mjedisit dhe Planifikimit Hapësinor /Ministarstv Sredine i Prstrng Planiranja*  
AGJENCIJA KADASTRALE E KOSOVËS/KATASTARSKA AGENCIJA KOSOVA

## Situacion i terrenit

Zyra kadastrale kmunale / pštinska katastarska kancelarija: Ferizaj  
Zona kadastrale / Katastarska zona: Ferizaj  
Nr. i njësisë kadastrale / Br. katastarske jedinice : 02966-1  
Numri i lëndës / Broj predmeta:  
Shkalla e zvoglimit / Razmëra plana 1: 150

#### **Lista e koordinatave të pikave të matura:**

Nr	Y	X	H	DSC
88	7510622.908	4693458.842	646,236	ard_fr_p2
89	7510600.968	4693466.253	642,582	ard_fr_p3
90	7510642.920	4693459.301	651,631	ard_fr_p4
91	7510657.311	4693459.617	651,229	ard_fr_p5
92	7510657.975	4693474.073	651,220	ard_fr_p6
93	7510655.734	4693495.242	645,569	arm_f_p1
94	7510637.813	4693483.888	646,943	arm_f_s1
95	7510637.817	4693483.863	656,999	arm_f_s2
96	7510650.640	4693468.625	653,133	arm_f_s4
78	7510644.470	4693469.312	656,029	kulmi
86	7510638.853	4693484.798	645,880	kygje-uj
36	7510641.829	4693478.618	648,248	perdthese
37	7510639.703	4693477.364	648,248	perdthese
38	7510639.232	4693465.791	648,248	perdthese
39	7510638.001	4693465.065	648,248	perdthese
40	7510632.905	4693473.355	648,248	perdthese
97	7510639.271	4693465.772	648,248	perdthese
98	7510641.077	4693466.793	648,248	perdthese
99	7510641.04	4693466.86	648,248	perdthese
100	7510645	4693469.2	648,248	perdthese
101	7510644.65	4693469.78	648,248	perdthese
102	7510646.46	4693470.85	648,248	perdthese
19	7510638.74	4693478.99	648,212	perdthese-teras
20	7510631.89	4693475.01	648,248	perdthese-teras
59	7510655.06	4693496.04	645,569	pusefekale
1	7510668.36	4693477.25	651,085	shtylelektrike
79	7510638.42	4693464.35	654,347	strehra
80	7510641.47	4693466.17	654,347	strehra

Shpjegues

- |  |                                   |                           |
|--|-----------------------------------|---------------------------|
|  | Kufiri kadastral (nga SIKTK-G)    | Pikë e objekteve riqnjë   |
|  | Ndërtesa në trajtim për legalizim | Emri i rrugës             |
|  | Ndërtesa tjera                    | Pikë e rrjetës gjeodezike |
|  | Aneks Ndërtimi                    | Pikë e strehëve           |
|  | Shtyllë elektrike                 | Pikë e terasës            |
|  | Pusetë e ujësjellësit             | Pikë e objektit           |
|  | Pusetë e ujërave të zeza          | Pikë e murit              |
|  | Strehët                           | Pikë e kulmit             |
|  | Kyqje në rrymë                    |                           |

Rilevoi / Snimi: LIRIDON SEJDIU

(emri dhe mbiemri i gjedetit/kompanisë/ ime i prezime gedeta/ k

Nr. i licencës / Br. licence: 140

5. \_\_\_\_\_



Republika e Kosovës

Qeveria - Vlada



Ministria e Mjedisit dhe Planifikimit Hapësinor / Ministarstv Sredine i Prstrig Planiranja  
AGJENCIJA KADASTRALE E KOSOVËS / KATASTARSKA AGENCIJA KOSOVA

### Situacioni i terrenit

Zyra kadastrale kmunale / pëtinska katastarska kancelarija: Ferizaj

Zona kadastrale / Katastarska zona: Ferizaj

Nr. i njësisë kadastrale / Br. katastarske jedinice : 02966-1

Numri i lëndës / Broj predmeta: \_\_\_\_\_

Shkalla e zvoglimit / Razmera plana 1: 150

### Lista e koordinatave të pikave të matura:

Nr	Y	X	H	DSC
88	7510622.908	4693458.842	646.236	ard_fr_p2
89	7510600.989	4693466.253	642.582	ard_fr_p3
90	7510642.920	4693459.301	651.363	ard_fr_p4
91	7510657.311	4693459.617	651.229	ard_fr_p5
92	7510675.977	4693474.073	651.220	ard_fr_p6
93	7510655.734	4693495.242	645.569	arm_f_p1
94	7510637.813	4693483.888	646.943	arm_fr_fs1
95	7510637.817	4693483.863	646.969	arm_fr_fs2
96	7510650.640	4693468.626	653.133	arm_fr_p4
78	7510644.470	4693469.312	656.029	kulmi
86	7510638.853	4693484.798	645.889	kyqje-uj
36	7510641.829	4693478.618	648.248	perdhese
37	7510639.703	4693477.364	648.248	perdhese
38	7510639.232	4693465.727	648.248	perdhese
39	7510638.001	4693465.065	648.248	perdhese
40	7510632.905	4693473.355	648.248	perdhese
97	7510639.271	4693465.727	648.248	perdhese
98	7510641.077	4693466.793	648.248	perdhese
99	7510641.038	4693466.857	648.248	perdhese
100	7510645.005	4693469.197	648.248	perdhese
101	7510644.645	4693469.782	648.248	perdhese
102	7510646.463	4693470.855	648.248	perdhese



### Shpjegues:

Kufiri kadastral (nga SIKTK-G)

Ndërtesa në trajtim për legalizim

Ndërtesa tjera

Aneks Ndërtimi

Shtyllë elektrike

Pusetë e ujësjellësit

Pusetë e ujërave të zeza

Strehët

Kyqje në rrymë

Rilevoi / Snimi: LIRIDON SEJDIU

(emri dhe mbiemri i gjedjetit/kompanisë / ime i prezime gedeta/ kompanije)

Nr. i licencës / Br. licence: 140

Data e rilevimit / Datum snimanja: 19.07.2025

Nënshkrimi / Potpis: \_\_\_\_\_

v.v.

Pikë e objekteve fqinje

Emri i rrugës

Pikë e rrjetës gjeodezike

Pikë e strehëve

Pikë e terasës

Pikë e objektit

Pikë e murit

Pikë e kulmit

81

10

0

■



Republika e Kosovës  
Republika Kosova-Republic of Kosovo  
Qeveria e Kosovës- Vlada Kosova- Government of Kosovo  
Ministria e Infrastrukturës dhe Ambientit/ Ministrastvo Infrastrukture i Sredine/ Ministry of Infrastructure and Environment  
AGJENCIA KADASTRALE E KOSOVËS/KOSOVSKA KATASTARSKA AGENCIJA/ KOSOVO CADASTRAL AGENCY

<b>Komuna:</b> Ferizaj	<b>Zona Kadastrale:</b> Ferizaj
<b>Numri i njësis kadastrale:</b> 02966-1	<b>Sistemi koordinat:</b> KosovaRef01

Nr	Y	X	H	Kodi	Përshkrimi	Burimi
19	7510638.742	4693478.994	648.212	40	Shtëpi-Ndërtesë	PM
20	7510631.890	4693475.006	648.248	40	Shtëpi-Ndërtesë	PM
36	7510641.829	4693478.618	648.248	40	Shtëpi-Ndërtesë	PM
37	7510639.703	4693477.364	648.248	40	Shtëpi-Ndërtesë	PM
38	7510639.232	4693465.791	648.248	40	Shtëpi-Ndërtesë	PM
39	7510638.001	4693465.065	648.248	40	Shtëpi-Ndërtesë	PM
40	7510632.905	4693473.355	648.248	40	Shtëpi-Ndërtesë	PM
97	7510639.271	4693465.727	648.248	40	Shtëpi-Ndërtesë	PM
98	7510641.077	4693466.793	648.248	40	Shtëpi-Ndërtesë	PM
99	7510641.038	4693466.857	648.248	40	Shtëpi-Ndërtesë	PM
100	7510645.005	4693469.197	648.248	40	Shtëpi-Ndërtesë	PM
101	7510644.645	4693469.782	648.248	40	Shtëpi-Ndërtesë	PM
102	7510646.463	4693470.855	648.248	40	Shtëpi-Ndërtesë	PM

Gjeodeti / Kompania gjeodete e licencuar:	Liridon Sejdiu	Nënshkrimi dhe vula:	
Numri i licencës	140		

Shfaq	Zgjedhur	Resultatet	Shkarko	
	ParcelDetailId	CadastreUnitId	CadastreZoneId	C
<input type="checkbox"/>	11160175	P-72217092-0...	72217092	7...
<input checked="" type="checkbox"/>	11160175	P-72217092-0...	72217092	7...

Vendos né objekt Zmazho né objekt

Detajet


ParcelDetailId: 11160175

CadastreUnitId: P-72217092-02966-1

CadastreZoneId: 72217092

CadastreZo

## Geometry:

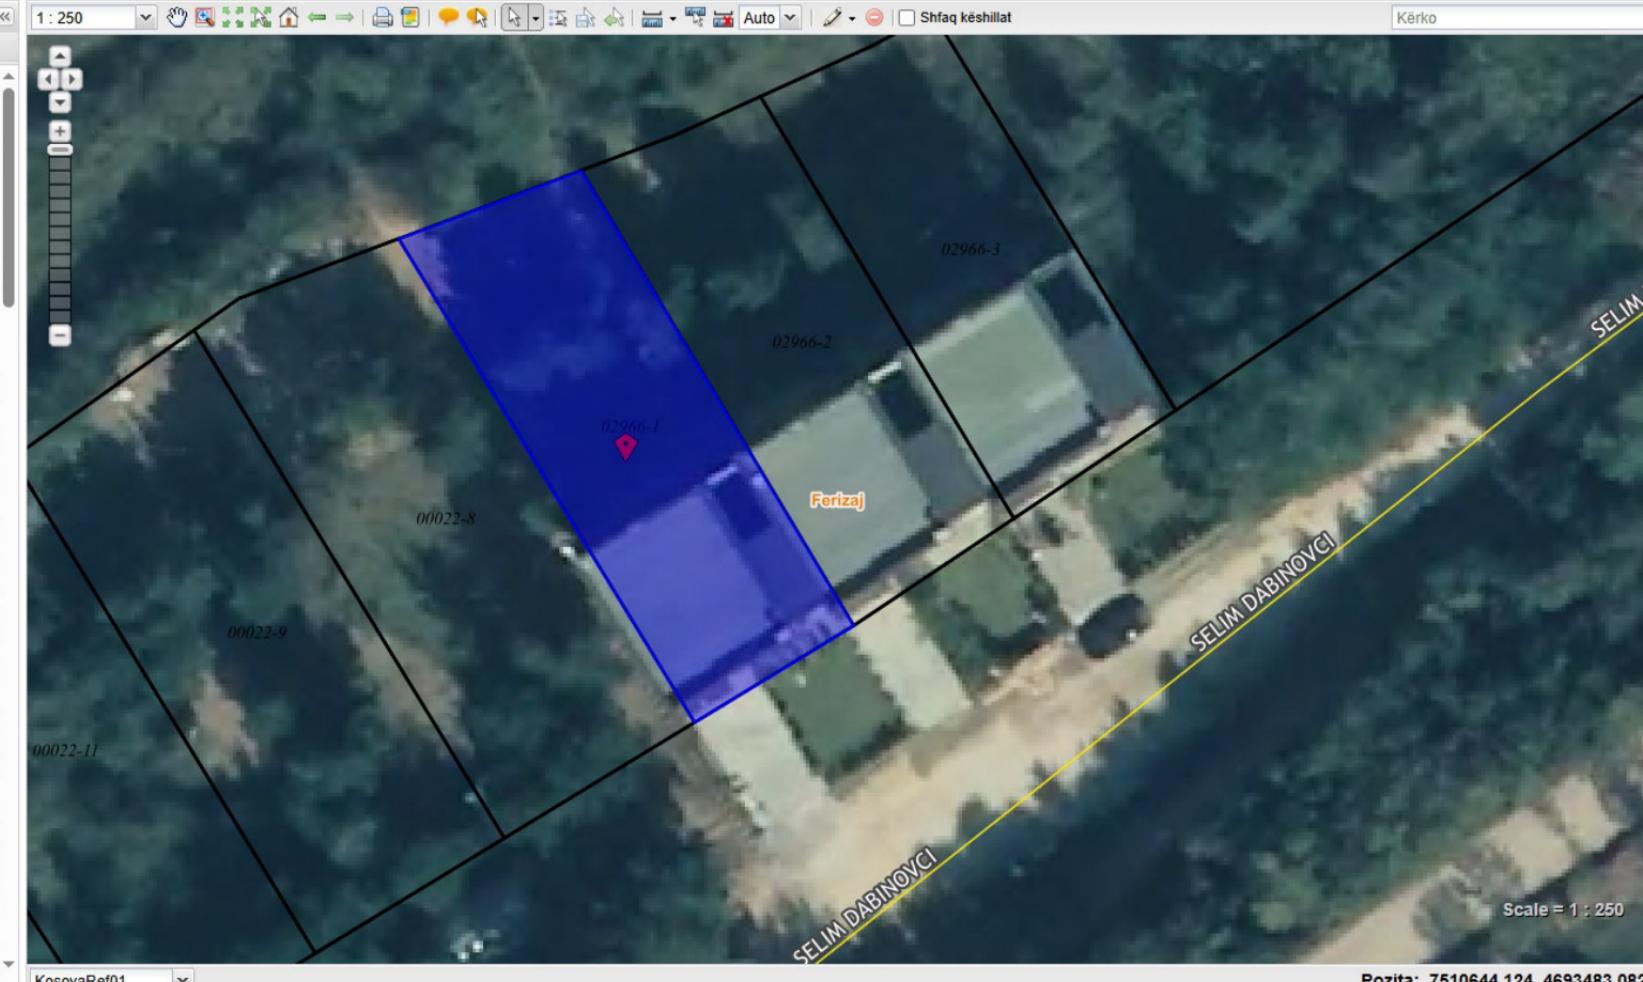

Zyra kadastrale komunale / Opštinska katastarska kancelarija: FerizajNr. i njësisë kadastrale / Br. katastarske jedinice : 02966-1Zona kadastrale / Katastarska zona: Ferizaj

Numri i lëndës / Broj predmeta: \_\_\_\_\_

Lloji i njësisë kadastrale / Vrsta katastarske jedinice : ShtëpiShkalla e zvoglimit / Razmera plana 1: 150**Republika e Kosovës**

Republika Kosova-Republic of Kosovo

Qeveria -Vlada-Government

Ministria e Mjedisit dhe Planifikimit Hapësinor /Ministarstvo Sredine i Prostornog Planiranja/Ministry of Environment and Spatial Planning

AGJENCIA KADASTRALE E KOSOVËS/KATASTARSKA AGECIJA KOSOVA/KOSOVA CADASTRAL AGENCY



Terasa

02966-3

02966-1

Terasa

B+P+1

02966-2

Rr. "Selim Dabinovci"

Bodrumi  
O-72217092-  
49.24 m<sup>2</sup>

2

3

-0

123

4

122

121

120

114

Nr.	Y	X	H	D	Etazhi	Sqarim	Sipërfaqja (m <sup>2</sup> )
2	7510632.92	4693473.32	645.94	bodrum	Bodrumi	Bodrumi	49.24
3	7510635.39	4693469.32	645.94	bodrum			
4	7510639.25	4693477.09	645.90	bodrum			
114	7510644.29	4693474.50	645.94	bodrum			
120	7510641.74	4693478.77	645.94	bodrum			
121	7510639.69	4693477.58	645.94	bodrum			
122	7510639.80	4693477.41	645.94	bodrum			
123	7510639.28	4693477.03	645.94	bodrum	Gjithsej:	Gjithsej:	49.24

Rilevoi / Snimio: LIRIDON SEJDIU  
(emri dhe mbiemri i gjydetit/kompanisë/ ime i prezime geodeta/ kompanije)Aprovoi / Usvojio: \_\_\_\_\_  
(emri dhe mbiemri i pësonit zyrtar/ ime i prezime sluzbeneg lica)Nr. i licencës / Br. licence: 140

V.V.

Nënshkrimi / Potpis: \_\_\_\_\_

Nënshkrimi / Potpis: \_\_\_\_\_

Data e rilevimit / Datum snimanja: 19.07.2025

Data e rilevimit / Datum snimanja: \_\_\_\_\_



Nr.	Y	X	H	D	Etazhi	Sqarim	Sipërfaqja (m <sup>2</sup> )
36	7510641.83	4693478.62	648.25	perdhese	Përdhesa	Përdhesa	98.89
37	7510639.70	4693477.36	648.25	perdhese			
38	7510639.23	4693465.79	648.25	perdhese			
39	7510638.00	4693465.06	648.25	perdhese			
40	7510632.90	4693473.36	648.25	perdhese			
97	7510639.27	4693465.73	648.25	perdhese			
98	7510641.08	4693466.79	648.25	perdhese			
99	7510641.04	4693466.86	648.25	perdhese			
100	7510645.00	4693469.20	648.25	perdhese		Terasa	15.15
101	7510644.65	4693469.78	648.25	perdhese			
102	7510646.46	4693470.85	648.25	perdhese	Gjithsej:	114.04	
19	7510638.74	4693478.99	648.21	perdhese-terasa			
20	7510631.89	4693475.01	648.25	perdhese-terasa			

Rilevoi / Snimio: LIRIDON SEJDIU  
(emri dhe mbiemri i gjeodetit/kompanisë/ ime i prezime geodeta/ kompanije)

Aprovoi / Usvojio: \_\_\_\_\_  
(emri dhe mbiemri i përsonit zyrtar/ ime i prezime sluzbenog lica)

Nr. i licencës / Br. licence: 140

V.V.

Nënshkrimi / Potpis: \_\_\_\_\_

Nënshkrimi / Potpis: \_\_\_\_\_

Data e rilevimit / Datum snimania: 19.07.2025

Data e rilevimit / Datum snimanja:

Zyra kadastrale komunale / Opštinska katastarska kancelarija: FerizajNr. i njësisë kadastrale / Br. katastarske jedinice : 02966-1Zona kadastrale / Katastarska zona: Ferizaj

Numri i lëndës / Broj predmeta: \_\_\_\_\_

Lloji i njësisë kadastrale / Vrsta katastarske jedinice : ShtëpiShkalla e zvoglimit / Razmera plana 1: 150**Republika e Kosovës**

Republika Kosova-Republic of Kosovo

Qeveria -Vlada-Government

Ministria e Mjedisit dhe Planifikimit Hapësinor /Ministarstvo Sredine i Prostornog Planiranja/Ministry of Environment and Spatial Planning

AGJENCIA KADASTRALE E KOSOVËS/KATASTARSKA AGECIJA KOSOVA/KOSOVA CADASTRAL AGENCY



Terasa

02966-3


02966-1

Terasa

B+P+1

02966-2

Rr. "Selim Dabinovci"

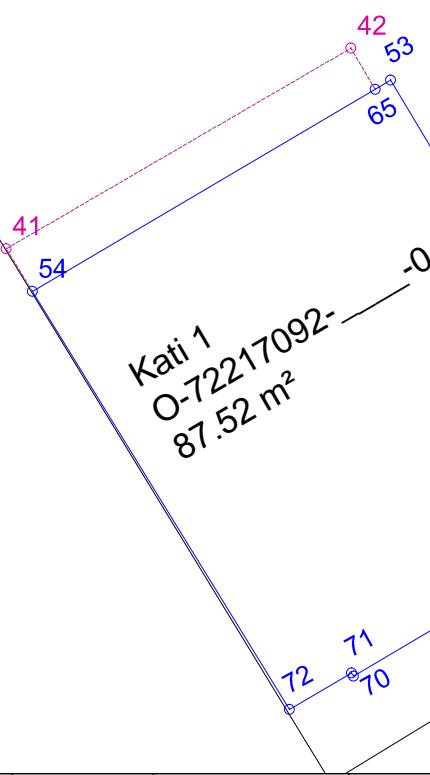

Nr.	Y	X	H	D	Etazhi	Sqarim	Sipërfaqja (m <sup>2</sup> )
53	7510640.01	4693477.55	651.39	katil	Kati 1	Kati 1	79.84
54	7510632.90	4693473.36	651.39	katil			
65	7510639.70	4693477.36	651.39	katil			
67	7510644.97	4693469.21	651.39	katil			
68	7510641.04	4693466.86	651.39	katil			
69	7510641.08	4693466.79	651.39	katil			
70	7510639.27	4693465.73	651.39	katil			
71	7510639.23	4693465.79	651.39	katil			
72	7510638.00	4693465.06	651.39	katil			
41	7510632.38	4693474.20	651.39	katil terasa			
42	7510639.22	4693478.18	651.39	katil terasa		Gjithsej:	87.52

Rilevoi / Snimio: LIRIDON SEJDIU  
(emri dhe mbiemri i gjykozit/kompanisë/ ime i prezime geodeta/ kompanije)Aprovoi / Usvojio: \_\_\_\_\_  
(emri dhe mbiemri i pësonit zyrtar/ ime i prezime sluzbeneg lica)Nr. i licencës / Br. licence: 140

V.V.

Nënshkrimi / Potpis: \_\_\_\_\_

Nënshkrimi / Potpis: \_\_\_\_\_

Data e rilevimit / Datum snimanja: 19.07.2025

Data e rilevimit / Datum snimanja: \_\_\_\_\_



Republika e Kosovës

Republika Kosova-Republic of Kosovo

Qeveria e Kosovës- Vlada Kosova- Government of Kosovo

Ministria e Infrastrukturës dhe Ambientit/ Ministrastvo Infrastrukture i Sredine/ Ministry of Infrastructure and Environment

AGJENCIA KADASTRALE E KOSOVËS/KOSOVSKA KATASTARSKA AGENCIJA/ KOSOVO CADASTRAL AGENCY

**Komuna: Ferizaj**

**Numri i njësis kadastrale: 00925-41**

**Zona Kadastrale: Ferizaj**

**Sistemi koordinat: KosovaRef01**

Nr.	Y	X	H	D	Etazhi	Sqarim	Sipërfaqja (m <sup>2</sup> )
36	7510641.83	4693478.62	648.25	perdhese	Përdhesa		98.89
37	7510639.70	4693477.36	648.25	perdhese			
38	7510639.23	4693465.79	648.25	perdhese			
39	7510638.00	4693465.06	648.25	perdhese			
40	7510632.90	4693473.36	648.25	perdhese			
97	7510639.27	4693465.73	648.25	perdhese			
98	7510641.08	4693466.79	648.25	perdhese			
99	7510641.04	4693466.86	648.25	perdhese			
100	7510645.00	4693469.20	648.25	perdhese			
101	7510644.65	4693469.78	648.25	perdhese			
102	7510646.46	4693470.85	648.25	perdhese	Terasa	15.15	
19	7510638.74	4693478.99	648.21	perdhese-terasa			
20	7510631.89	4693475.01	648.25	perdhese-terasa	Gjithsej:	114.04	

Nr.	Y	X	H	D	Etazhi	Sqarim	Sipërfaqja (m <sup>2</sup> )
53	7510640.01	4693477.55	651.39	kati1	Kati 1		79.84
54	7510632.90	4693473.36	651.39	kati1			
65	7510639.70	4693477.36	651.39	kati1			
67	7510644.97	4693469.21	651.39	kati1			
68	7510641.04	4693466.86	651.39	kati1			
69	7510641.08	4693466.79	651.39	kati1			
70	7510639.27	4693465.73	651.39	kati1			
71	7510639.23	4693465.79	651.39	kati1			
72	7510638.00	4693465.06	651.39	kati1			
41	7510632.38	4693474.20	651.39	kati1 terasa			
42	7510639.22	4693478.18	651.39	kati1 terasa	Gjithsej:	87.52	

Nr.	Y	X	H	D	Etazhi	Sqarim	Sipërfaqja (m <sup>2</sup> )
2	7510632.92	4693473.32	645.94	bodrum	Bodrumi		49.24
3	7510635.39	4693469.32	645.94	bodrum			
4	7510639.25	4693477.09	645.90	bodrum			
114	7510644.29	4693474.50	645.94	bodrum			
120	7510641.74	4693478.77	645.94	bodrum			
121	7510639.69	4693477.58	645.94	bodrum			
122	7510639.80	4693477.41	645.94	bodrum			
123	7510639.28	4693477.03	645.94	bodrum			
					Gjithsej:	49.24	

Gjeodeti / Kompania gjeodete e licencuar:	Liridon Sejdiu	Nënshkrimi dhe vula:	
Numri i licencës	140		



02966-1

02966-3

02966-2

Terasa

B+P+1  
O-72217092  
114.04 m<sup>2</sup>

Rr. "Selim Dabinovci"



Nr	Y	X	H	Kodi	Përshkrimi	Burimi
19	7510638.742	4693478.994	648.212	40	Shtëpi-Ndërtesë	PM
20	7510631.890	4693475.006	648.248	40	Shtëpi-Ndërtesë	PM
36	7510641.829	4693478.618	648.248	40	Shtëpi-Ndërtesë	PM
37	7510639.703	4693477.364	648.248	40	Shtëpi-Ndërtesë	PM
38	7510639.232	4693465.791	648.248	40	Shtëpi-Ndërtesë	PM
39	7510638.001	4693465.065	648.248	40	Shtëpi-Ndërtesë	PM
40	7510632.905	4693473.355	648.248	40	Shtëpi-Ndërtesë	PM
97	7510639.271	4693465.727	648.248	40	Shtëpi-Ndërtesë	PM
98	7510641.077	4693466.793	648.248	40	Shtëpi-Ndërtesë	PM
99	7510641.038	4693466.857	648.248	40	Shtëpi-Ndërtesë	PM
100	7510645.005	4693469.197	648.248	40	Shtëpi-Ndërtesë	PM
101	7510644.645	4693469.782	648.248	40	Shtëpi-Ndërtesë	PM
102	7510646.463	4693470.855	648.248	40	Shtëpi-Ndërtesë	PM

Rilevoi / Snimio: LIRIDON SEJDIU  
(emri dhe mbiemri i gjyqetarit/kompanisë/ ime i prezime geodeta/ kompanije)Aprovoi / Usvojio: \_\_\_\_\_  
(emri dhe mbiemri i pësonit zyrtar/ ime i prezime sluzbeneg lica)

Nr. i licencës / Br. licence: 140

V.V.

Nënshkrimi / Potpis: \_\_\_\_\_

Nënshkrimi / Potpis: \_\_\_\_\_

Data e rilevimit / Datum snimanja: 19.07.2025

Data e rilevimit / Datum snimanja: \_\_\_\_\_



Republika e Kosovës  
Republika Kosova-Republic of Kosovo  
Qeveria e Kosovës- Vlada Kosova- Government of Kosovo  
Ministria e Infrastrukturës dhe Ambientit/ Ministrastvo Infrastrukture i Sredine/ Ministry of Infrastructure and Environment  
AGJENCIA KADASTRALE E KOSOVËS/KOSOVSKA KATASTARSKA AGENCIJA/ KOSOVO CADASTRAL AGENCY

<b>Komuna:</b> Ferizaj	<b>Zona Kadastrale:</b> Ferizaj
<b>Numri i njësis kadastrale:</b> 02966-1	<b>Sistemi koordinat:</b> KosovaRef01

Nr	Y	X	H	Kodi	Përshkrimi	Burimi
19	7510638.742	4693478.994	648.212	40	Shtëpi-Ndërtesë	PM
20	7510631.890	4693475.006	648.248	40	Shtëpi-Ndërtesë	PM
36	7510641.829	4693478.618	648.248	40	Shtëpi-Ndërtesë	PM
37	7510639.703	4693477.364	648.248	40	Shtëpi-Ndërtesë	PM
38	7510639.232	4693465.791	648.248	40	Shtëpi-Ndërtesë	PM
39	7510638.001	4693465.065	648.248	40	Shtëpi-Ndërtesë	PM
40	7510632.905	4693473.355	648.248	40	Shtëpi-Ndërtesë	PM
97	7510639.271	4693465.727	648.248	40	Shtëpi-Ndërtesë	PM
98	7510641.077	4693466.793	648.248	40	Shtëpi-Ndërtesë	PM
99	7510641.038	4693466.857	648.248	40	Shtëpi-Ndërtesë	PM
100	7510645.005	4693469.197	648.248	40	Shtëpi-Ndërtesë	PM
101	7510644.645	4693469.782	648.248	40	Shtëpi-Ndërtesë	PM
102	7510646.463	4693470.855	648.248	40	Shtëpi-Ndërtesë	PM

Gjeodeti / Kompania gjeodete e licencuar:	Liridon Sejdiu	Nënshkrimi dhe vula:	
Numri i licencës	140		



Republika e Kosovës

Republika Kosova - Republic of Kosovo

Qeveria e Kosovës - Vlada Kosova - Government of Kosovo

Ministria e Infrastrukturës dhe Ambientit/ Ministrastvo Infrastrukture i Sredine/ Ministry of Infrastructure and Environment

AGJENCIA KADASTRALE E KOSOVËS/ KOSOVSKA KATASTARSKA AGENCIJA/ KOSOVA CADASTRAL AGENCY

R E G J I S T R I M I I N DERTESËS / SHTËPISË													
Nr	Komuna	Zona Kadastrale	Numri i ndërtesës (njësia)	Etazhiteti	Katet	Sipërfaqja e kateve [m <sup>2</sup> ]	Sipërfaqja e bazamentit [m <sup>2</sup> ]	Adresa e Njësisë	Vendi i quajtur	Shfrytëzimi i aktual	Pronari / Shfrytëzuesi Emri (Emri i prindit) Mbiemri	Numri përsoneal	Pjesa e Pronës
1	Ferizaj	Ferizaj	O-72217092-_____0	B+P+1	Bodrumi Përdhesa Kati 1 Gjithsej:	49.24 114.04 87.52 250.80	98.89	Rr. "Selim Dabinovci" Ferizaj	KODRA E KAZERMËS	Banim	Armend (Habil) Dabinovci	1005004957	1/1

Gjeodeti/kompania e licencuar: LIRIDON SEJDIU

Nr i licencës: 140

Nënshkrimi dhe vula:

















