

Nr	Y	X	H	Kodi	Përshtkimi	Burimi
25	7510662.596	4693480.525	648.248	40	Shtëpi-Ndërtesë	PM
26	7510659.761	4693489.987	648.248	40	Shtëpi-Ndërtesë	PM
27	7510662.412	4693480.841	648.248	40	Shtëpi-Ndërtesë	PM
28	7510657.565	4693488.655	648.248	40	Shtëpi-Ndërtesë	PM
29	7510664.392	4693482.042	648.248	40	Shtëpi-Ndërtesë	PM
30	7510650.670	4693484.474	648.248	40	Shtëpi-Ndërtesë	PM
109	7510658.660	4693478.138	648.248	40	Shtëpi-Ndërtesë	PM
110	7510658.725	4693478.027	648.248	40	Shtëpi-Ndërtesë	PM
111	7510656.985	4693476.971	648.248	40	Shtëpi-Ndërtesë	PM
112	7510656.434	4693477.917	648.248	40	Shtëpi-Ndërtesë	PM
113	7510655.087	4693477.101	648.248	40	Shtëpi-Ndërtesë	PM
23	7510649.643	4693486.188	648.248	40	Shtëpi-Ndërtesë	PM
24	7510656.560	4693490.312	648.181	40	Shtëpi-Ndërtesë	PM



Republika e Kosovës  
Qeveria - Vlada  
Ministria e Mjedisit dhe Planifikimit Hapësinor /Ministarstv Sredine i Prstrg Planiranja  
AGJENCIJA KADASTRALE E KOSOVËS / KATASTARSKA AGENCJA KOSOVA



### Situacioni i terrenit

Zyra kadastrale kmunale / pëtinska katastarska kancelarija: Ferizaj

Zona kadastrale / Katastarska zona: Ferizaj

Nr. i njësisë kadastrale / Br. katastarske jedinice : 02966-3

Numri i lëndës / Broj predmeta:

Shkalla e zvoglimit / Razmera plana 1: 150

### Lista e koordinatave të pikave të matura:

Nr	Y	X	H	DSC
88	7510622.908	4693458.842	646.236	ard_fr_p2
89	7510600.989	4693466.253	642.582	ard_fr_p3
90	7510642.920	4693459.301	651.363	ard_fr_p4
91	7510657.311	4693459.617	651.229	ard_fr_p5
92	7510675.977	4693474.073	651.220	ard_fr_p6
93	7510655.734	4693495.242	645.569	arm_f_p1
94	7510637.813	4693483.888	646.943	arm_fr_fs1
95	7510637.817	4693483.863	646.969	arm_fr_fs2
96	7510650.640	4693468.626	653.133	arm_fr_fs4
55	7510653.600	4693486.605	656.195	kulmi
77	7510661.747	4693480.470	656.196	kulmi
354	7510638.853	4693484.798	645.889	kyqje-uj
25	7510662.596	4693480.525	648.248	perdhese
26	7510659.761	4693489.987	648.248	perdhese
27	7510662.412	4693480.841	648.248	perdhese
28	7510657.565	4693488.655	648.248	perdhese
29	7510664.392	4693482.042	648.248	perdhese
30	7510650.670	4693484.474	648.248	perdhese
109	7510658.660	4693478.138	648.248	perdhese
110	7510658.725	4693478.027	648.248	perdhese
111	7510656.985	4693476.971	648.248	perdhese
112	7510656.434	4693477.917	648.248	perdhese
113	7510655.087	4693477.101	648.248	perdhese
114	7510656.560	4693490.312	648.181	perdhese
115	7510656.599	4693476.97	648.248	perdhese
116	7510656.443	4693477.92	648.248	perdhese
117	7510655.09	4693477.1	648.248	perdhese
118	7510655.09	4693477.1	648.248	perdhese
119	7510649.64	4693486.19	648.248	perdhese-terasa
120	7510656.556	4693490.31	648.181	perdhese-terasa
121	7510655.06	4693496.04	645.569	pusefekale
122	7510658.36	4693477.25	651.085	shtyElektrike
123	7510656.1	4693475.61	654.342	streha
124	7510658.95	4693477.31	654.523	streha

### Shpjegues:

- Kufiri kadastral (nga SIKTK-G)
- Ndërtesa në trajtim për legalizim
- Ndërtesa tjera
- △ Aneks Ndërtimi
- ▲ Shtyllë elektrike
- Pusetë e ujësjellësit
- Pusetë e ujërave të zeza
- Strehët
- ④ Kyqje në rrymë

Rilevoi / Snimi: LIRIDON SEJDIU

(emri dhe mbiemri i gjedhit/kompanisë / ime i prezime gedeta/ kompanije)

Nr. i licencës / Br. licence: 140

Data e rilevimit / Datum snimanja: 19.07.2025

Nënshkrimi / Potpis: \_\_\_\_\_

V.V.

Nr	Y	X	H	Kodi	Përkrimi	Burimi
25	7510662.596	4693480.525	648.248	40	Shtëpi-Ndërtesë	PM
26	7510659.761	4693489.987	648.248	40	Shtëpi-Ndërtesë	PM
27	7510662.412	4693480.841	648.248	40	Shtëpi-Ndërtesë	PM
28	7510657.565	4693488.655	648.248	40	Shtëpi-Ndërtesë	PM
29	7510664.392	4693482.042	648.248	40	Shtëpi-Ndërtesë	PM
30	7510650.670	4693484.474	648.248	40	Shtëpi-Ndërtesë	PM
109	7510658.660	4693478.138	648.248	40	Shtëpi-Ndërtesë	PM
110	7510658.725	4693478.027	648.248	40	Shtëpi-Ndërtesë	PM
111	7510656.985	4693476.971	648.248	40	Shtëpi-Ndërtesë	PM
112	7510656.434	4693477.917	648.248	40	Shtëpi-Ndërtesë	PM
113	7510655.087	4693477.101	648.248	40	Shtëpi-Ndërtesë	PM
23	7510649.643	4693486.188	648.248	40	Shtëpi-Ndërtesë	PM
24	7510656.560	4693490.312	648.181	40	Shtëpi-Ndërtesë	PM



**Republika e Kosovës**  
Qeveria - Vlada  
**Ministria e Mjedisit dhe Planifikimit Hapësinor/Ministarstv Sredine i Prstrg Planiranja**  
AGJENCIJA KADASTRALE E KOSOVËS / KATASTARSKA AGENCIJA KOSOVA

## Situacioni i terrenit

Zyra kadastrale kmunale / pštinska katastarska kancelarija: Ferizaj  
Zyra kadastrale / Kancelarija: Ferizaj

Zona kadastrale / Katastarska zona: Penza

Nr. i njësisë kadastrale / Br. katastarske jedinice : 02966-3

Numri i lëndës / Broj predmeta: \_\_\_\_\_

Shkalla e zvoglimit / Razmëra plana 1: 150

### **Lista e koordinatave të pikave të matura:**

Nr	Y	X	H	DSC
88	7510622.908	4693458.842	646.236	ard_fr_p2
89	7510600.989	4693466.253	642.582	ard_fr_p3
90	7510642.920	4693459.301	651.363	ard_fr_p4
91	7510657.917	4693459.617	651.229	ard_fr_p5
92	7510675.977	4693474.073	651.220	ard_fr_p6
93	7510655.734	4693495.242	645.569	arm_f_p1
94	7510637.817	4693488.888	646.943	arm_fr_fs1
95	7510637.817	4693483.863	646.999	arm_f_s2
96	7510650.640	4693468.626	653.133	arm_fr_f4
55	7510653.605	4693486.605	656.195	kulmi
77	7510661.747	4693480.470	656.196	kulmi
354	7510638.853	4693484.798	645.889	kyqje-uj
25	7510652.666	4693480.524	648.248	perdhease
26	7510659.761	4693489.987	648.248	perdhease
27	7510662.412	4693480.841	648.248	perdhease
28	7510657.655	4693488.655	648.248	perdhease
29	7510664.392	4693482.042	648.248	perdhease
30	7510650.670	4693484.474	648.248	perdhease
109	7510658.656	4693478.14	648.248	perdhease
110	7510658.73	4693478.03	648.248	perdhease
111	7510656.99	4693476.97	648.248	perdhease
112	7510655.43	4693477.92	648.248	perdhease
113	7510655.09	4693477.1	648.248	perdhease
23	7510649.64	4693486.19	648.248	perdhease-terasa
24	7510655.56	4693490.30	648.181	perdhease-terasa
353	7510655.06	4693496.04	645.569	pusetEkele
1	7510668.36	4693477.25	651.085	shtylElektrike
83	7510656.1	4693475.61	654.342	streha
84	7510658.95	4693477.31	654.523	streha

## **Shpjegues:**

- |                                   |                           |
|-----------------------------------|---------------------------|
| Kufiri kadastral (nga SIKTK-G)    | Pike e objekteve tçinje   |
| Ndërtesa në trajtim për legalizim | Rr. Emri i rrugës         |
| Ndërtesa tjera                    | Pikë e rrjetës gjeodezike |
| Aneks Ndërtimi                    | Pikë e strehëve           |
| Shtyllë elektrike                 | Pikë e terasës            |
| Pusetë e ujësjellësit             | Pikë e objektit           |
| Pusetë e ujërave të zeza          | Pikë e murit              |
| Strehët                           | Pikë e kulmit             |
| Kyqje në rrymë                    |                           |

Rilevoi / Snimi: LIRIDON SEJDIU

(emri dhe mbiemri i gjedjetit/kompanisë/ ime i prezime gedeta/ kompanije)

Nr. i licencës / Br. licence: 140

Data e rilevimit / Datum snimanja: 19.07.2025

Nënshtkrimi / Potpis:



Republika e Kosovës  
Republika Kosova-Republic of Kosovo  
Qeveria e Kosovës- Vlada Kosova- Government of Kosovo  
Ministria e Infrastrukturës dhe Ambientit/ Ministrastvo Infrastrukture i Sredine/ Ministry of Infrastructure and Environment  
AGJENCIA KADASTRALE E KOSOVËS/KOSOVSKA KATASTARSKA AGENCIJA/ KOSOVO CADASTRAL AGENCY

<b>Komuna:</b> Ferizaj	<b>Zona Kadastrale:</b> Ferizaj
<b>Numri i njësis kadastrale:</b> 02966-3	<b>Sistemi koordinat:</b> KosovaRef01

Nr	Y	X	H	Kodi	Përshkrimi	Burimi
25	7510662.596	4693480.525	648.248	40	Shtëpi-Ndërtesë	PM
26	7510659.761	4693489.987	648.248	40	Shtëpi-Ndërtesë	PM
27	7510662.412	4693480.841	648.248	40	Shtëpi-Ndërtesë	PM
28	7510657.565	4693488.655	648.248	40	Shtëpi-Ndërtesë	PM
29	7510664.392	4693482.042	648.248	40	Shtëpi-Ndërtesë	PM
30	7510650.670	4693484.474	648.248	40	Shtëpi-Ndërtesë	PM
109	7510658.660	4693478.138	648.248	40	Shtëpi-Ndërtesë	PM
110	7510658.725	4693478.027	648.248	40	Shtëpi-Ndërtesë	PM
111	7510656.985	4693476.971	648.248	40	Shtëpi-Ndërtesë	PM
112	7510656.434	4693477.917	648.248	40	Shtëpi-Ndërtesë	PM
113	7510655.087	4693477.101	648.248	40	Shtëpi-Ndërtesë	PM
23	7510649.643	4693486.188	648.248	40	Shtëpi-Ndërtesë	PM
24	7510656.560	4693490.312	648.181	40	Shtëpi-Ndërtesë	PM

Gjeodeti / Kompania gjeodete e licencuar:	Liridon Sejdiu	Nënshkrimi dhe vula:	
Numri i licencës	140		

## Rezultati i kërkimit

Shtafq	Zgjedhur	Rezultatet	Shkarko
ParcelDetailId	CadastreUnitId	CadastreZoneId	Ca
<input checked="" type="checkbox"/> 11160173	P-72217092-02...	72217092	72

Vendos në objekt  Zmadho në objekt

Numri i rezultateve: 1 (showing first 1)

Nga harta: 0

## Detajet

ParcelDetailId: 11160173

CadastreUnitId: P-72217092-02966-3

CadastreZoneId: 72217092

CadastreZoneCode: 72217092

## Geometry:

Status: 1

Sipërfaqja Grafike (m<sup>2</sup>): 279.8

Raport

## Lista e shtresës

Ndhima

- Ortofoto
  - Orthophoto2024Rural
  - Orthophoto2024Urban
  - Orthophoto2018Rural
  - Orthophoto2018Malore
  - Orthophoto2018Urban
  - Ortofoto 2015 UAV
  - Ortofoto 2012
  - Ortofoto 2009
  - Ortofoto 2004
- Hartat Topografike
  - Harta Topografike 1:250000
  - Harta Topografike 1:25000 (2015)
  - Nomenklatura
- Rindërtimi i Informacioneve Kadastrale
  - RIK\_2025
- Modeli Dixhital i Terrenit
  - Modeli Dixhital i Terrenit
- Rilevimi
  - Indeksi i Ortofotove Rurale 2024
  - Indeksi i Ortofotove Urbane 2024
  - Indeksi i Ortofotove 2018
- Rrjeti Rugor
  - Autostradë
  - Rugë Nacionalë
  - Rugë Rajonale
- Njësi Administrative
  - Kufiri Shtetëror
  - Kufijtë dhe Emrat e Komunave
  - Zonë urbane
- Njësítë Kadastrale
  - Zonal Kadastrale
  - Parcelat
  - Numri parcelës
  - Ndërtesat
  - Numri ndertesës
- Sistemi i Adresave
  - Rrugët

KosovaRef01

1 : 250

Auto

Shfaq këshillat

Kerko

00022-5



Zyra kadastrale komunale / Opštinska katastarska kancelarija: FerizajNr. i njësisë kadastrale / Br. katastarske jedinice : 02966-3Zona kadastrale / Katastarska zona: Ferizaj

Numri i lëndës / Broj predmeta: \_\_\_\_\_


Lloji i njësisë kadastrale / Vrsta katastarske jedinice : ShtëpiShkalla e zvoglimit / Razmera plana 1: 150**Republika e Kosovës**

Republika Kosova-Republic of Kosovo

Qeveria -Vlada-Government

Ministria e Mjedisit dhe Planifikimit Hapësinor /Ministarstvo Sredine i Prostornog Planiranja/Ministry of Environment and Spatial Planning

AGJENCIA KADASTRALE E KOSOVËS/KATASTARSKA AGECIJA KOSOVA/KOSOVA CADASTRAL AGENCY

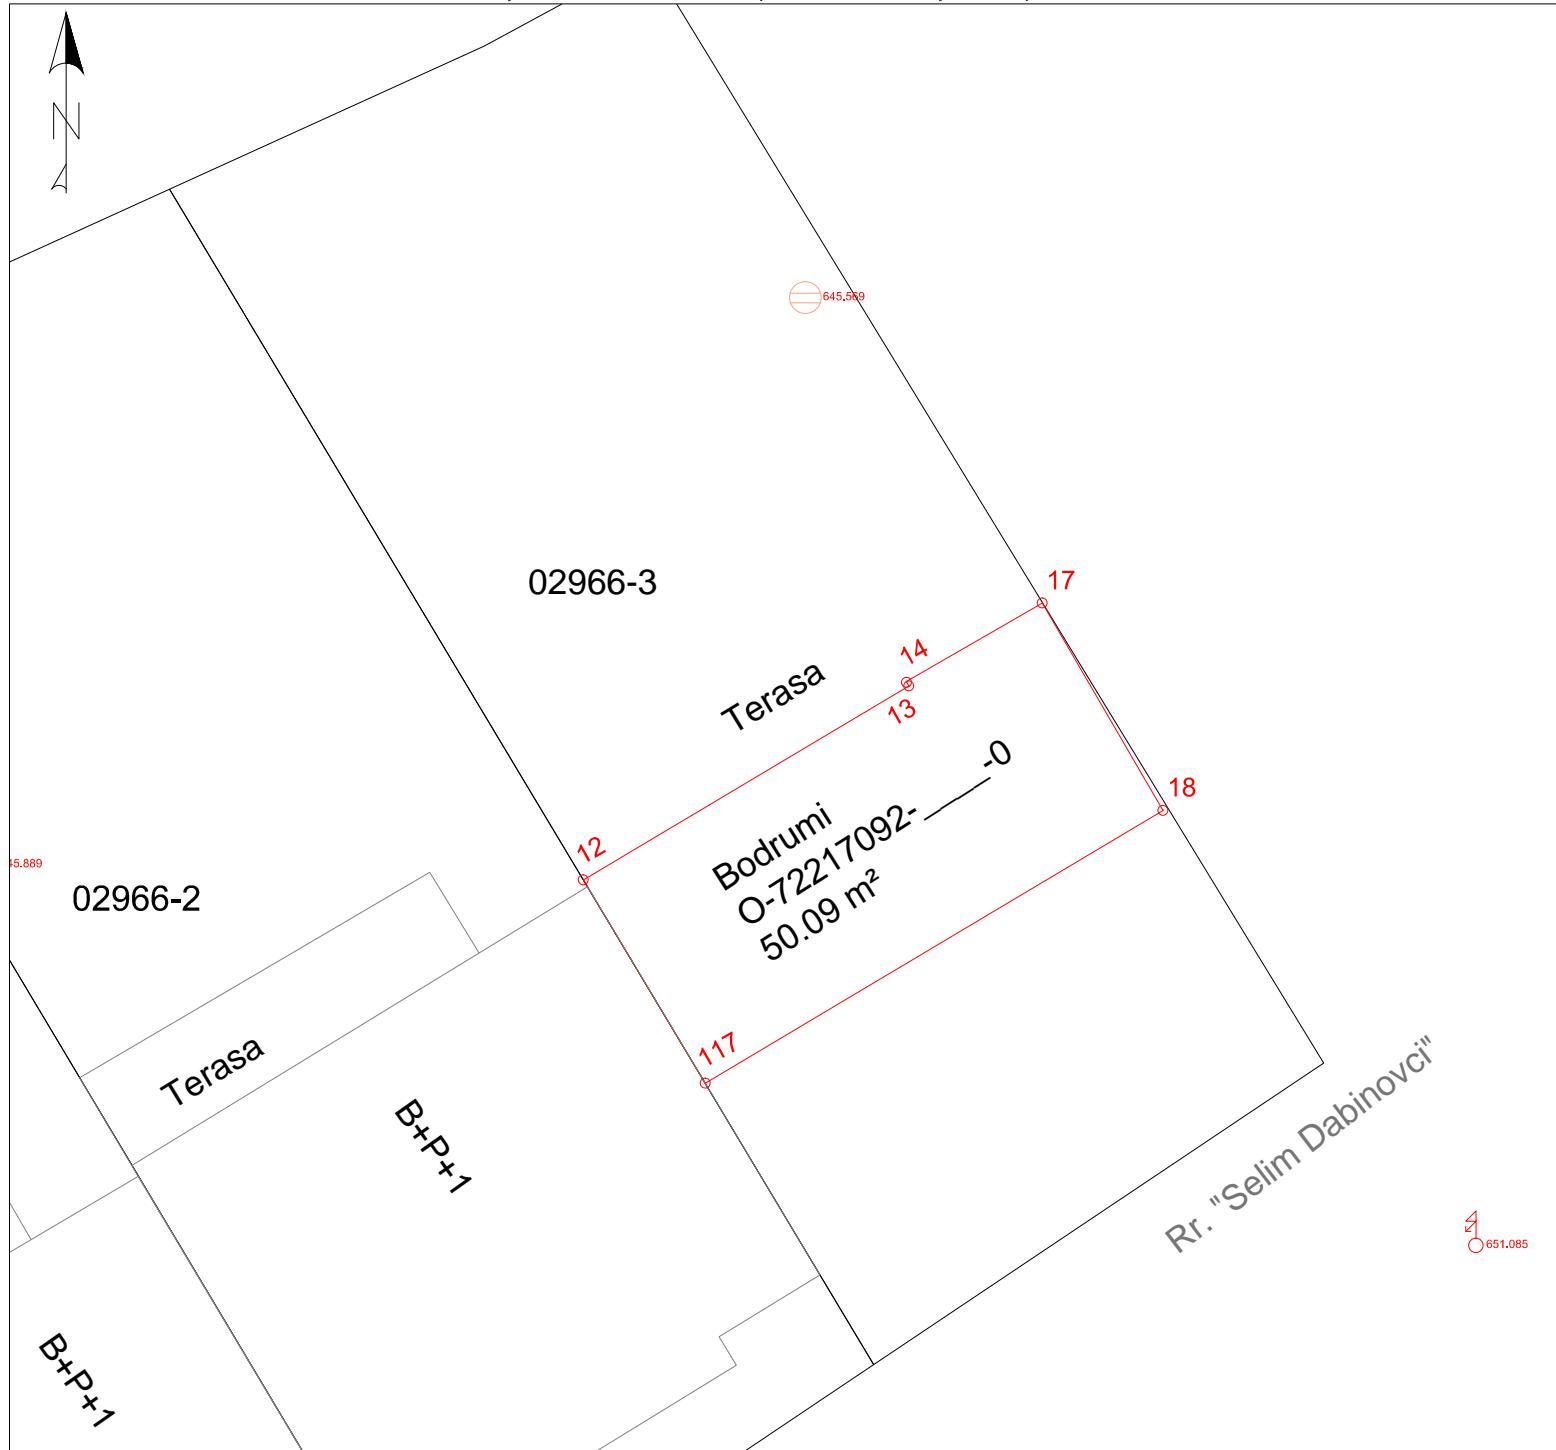

Nr.	Y	X	H	D	Etazhi	Sqarim	Sipërfaqja (m <sup>2</sup> )
12	7510650.66	4693484.49	645.94	bodrum	Bodrumi	Bodrumi	50.09
13	7510657.12	4693488.34	645.94	bodrum			
14	7510657.07	4693488.41	646.09	bodrum			
17	7510659.76	4693489.99	645.94	bodrum			
18	7510662.16	4693485.87	645.94	bodrum			
117	7510653.07	4693480.46	645.94	bodrum		Gjithsej:	50.09

Rilevoi / Snimio: LIRIDON SEJDIU  
(emri dhe mbiemri i gjyqetit/kompanisë/ ime i prezime geodeta/ kompanije)Aprovoi / Usvojio: \_\_\_\_\_  
(emri dhe mbiemri i pësonit zyrtar/ ime i prezime sluzbeneg lica)Nr. i licencës / Br. licence: 140

V.V.

Nënshkrimi / Potpis: \_\_\_\_\_

Nënshkrimi / Potpis: \_\_\_\_\_

Data e rilevimit / Datum snimanja: 19.07.2025

Data e rilevimit / Datum snimanja: \_\_\_\_\_

Zyra kadastrale komunale / Opštinska katastarska kancelarija: FerizajNr. i njësisë kadastrale / Br. katastarske jedinice : 02966-3Zona kadastrale / Katastarska zona: Ferizaj

Numri i lëndës / Broj predmeta: \_\_\_\_\_

Lloji i njësisë kadastrale / Vrsta katastarske jedinice : ShtëpiShkalla e zvoglimit / Razmera plana 1: 150**Republika e Kosovës****Republika Kosova-Republic of Kosovo****Qeveria -Vlada-Government****Ministria e Mjedisit dhe Planifikimit Hapësinor /Ministarstvo Sredine i Prostornog Planiranja/Ministry of Environment and Spatial Planning****AGJENCIA KADASTRALE E KOSOVËS/KATASTARSKA AGECIJA KOSOVA/KOSOVA CADASTRAL AGENCY**

Nr.	Y	X	H	D	Etazhi	Sqarim	Sipërfaqja (m <sup>2</sup> )
25	7510662.60	4693480.53	648.25	perdhese			
26	7510659.76	4693489.99	648.25	perdhese			
27	7510662.41	4693480.84	648.25	perdhese			
28	7510657.56	4693488.66	648.25	perdhese			
29	7510664.39	4693482.04	648.25	perdhese			
30	7510650.67	4693484.47	648.25	perdhese			
109	7510658.66	4693478.14	648.25	perdhese			
110	7510658.73	4693478.03	648.25	perdhese			
111	7510656.99	4693476.97	648.25	perdhese			
112	7510656.43	4693477.92	648.25	perdhese			
113	7510655.09	4693477.10	648.25	perdhese			
23	7510649.64	4693486.19	648.25	perdhese-terasa			
24	7510656.56	4693490.31	648.18	perdhese-terasa			
Përdhesa						Përdhesa	99.00
Terasa						Terasa	15.86
Gjithsej:							<b>114.86</b>

Rilevoi / Snimio: LIRIDON SEJDIU  
(emri dhe mbiemri i gjyqetit/kompanisë/ ime i prezime geodeta/ kompanije)Aprovoi / Usvojio: \_\_\_\_\_  
(emri dhe mbiemri i pësonit zyrtar/ ime i prezime sluzbeneg lica)Nr. i licencës / Br. licence: 140

V.V.

Nënshkrimi / Potpis: \_\_\_\_\_

Nënshkrimi / Potpis: \_\_\_\_\_

Data e rilevimit / Datum snimanja: 19.07.2025

Data e rilevimit / Datum snimanja: \_\_\_\_\_

**Republika e Kosovës** Shkallë  
Republika Kosova-Republic of Kosova  
Gjykatë Vlora, Gjykatë Gjenerale

*Ministria e Mjedisit dhe Planifikimit Hapësinor /Ministarstvo Sredine i Prostornog Planiranja/Ministry of Environment and Spatial Planning*  
AGJENCIJA KADASTRALE E KOSOVËS / KATASTARSKA AGEĆIJA KOSOVA / KOSOVA CADASTRAL AGENCY

AGENCIJA KADASTRALE E KOSOVES / KATASTARSKA AGENCIJA KOSOVA / KOSOVA CADASTRAL AGENCY



Nr.	Y	X	H	D	Etazhi	Sqarim	Sipërfaqja (m <sup>2</sup> )
47	7510657.78	4693488.79	651.39	katil	Kati 1	Kati 1	77.70
48	7510657.56	4693488.66	651.39	katil			
49	7510650.67	4693484.47	651.39	katil			
56	7510662.60	4693480.53	651.39	katil			
57	7510658.73	4693478.03	651.39	katil			
58	7510656.99	4693476.97	651.39	katil			
73	7510658.66	4693478.14	651.39	katil			
74	7510655.12	4693477.12	651.39	katil			
87	7510656.43	4693477.92	651.39	katil			
45	7510650.10	4693485.42	651.39	katil terasa			
46	7510657.02	4693489.55	651.39	katil terasa		Gjithsej:	86.36

Rilevoi / Snimio: LIRIDON SEJDIU  
(emri dhe mbiemri i gjyqetit/kompanisë/ ime i prezime geodeta/ kompanije)

Aprovoi / Usvojio: \_\_\_\_\_  
(emri dhe mbiemri i përsorit zyrtar/ ime i prezime sluzhenog lica)

Nr. i licencës / Br. licence: 140

V V

Nënshkrimi / Potpis:

Nënshtetës / Potpis: \_\_\_\_\_

Data e rilevimit / Datum snimanja: 19.07.2025

Data e rilevimit / Datum snimanja:



Republika e Kosovës

Republika Kosova-Republic of Kosovo

Qeveria e Kosovës- Vlada Kosova- Government of Kosovo

Ministria e Infrastrukturës dhe Ambientit/ Ministrastvo Infrastrukture i Sredine/ Ministry of Infrastructure and Environment

AGJENCIA KADASTRALE E KOSOVËS/KOSOVSKA KATASTARSKA AGENCIJA/ KOSOVO CADASTRAL AGENCY

**Komuna: Ferizaj**  
**Numri i njësis kadastrale: 02966-2**

**Zona Kadastrale: Ferizaj**  
**Sistemi koordinat: KosovaRef01**

Nr.	Y	X	H	D	Etazhi	Sqarim	Sipërfaqja (m <sup>2</sup> )
25	7510662.60	4693480.53	648.25	perdhese	Përdhesa	Përdhesa	99.00
26	7510659.76	4693489.99	648.25	perdhese			
27	7510662.41	4693480.84	648.25	perdhese			
28	7510657.56	4693488.66	648.25	perdhese			
29	7510664.39	4693482.04	648.25	perdhese			
30	7510650.67	4693484.47	648.25	perdhese			
109	7510658.66	4693478.14	648.25	perdhese			
110	7510658.73	4693478.03	648.25	perdhese			
111	7510656.99	4693476.97	648.25	perdhese			
112	7510656.43	4693477.92	648.25	perdhese			
113	7510655.09	4693477.10	648.25	perdhese			
23	7510649.64	4693486.19	648.25	perdhese-terasa	Terasa	15.86	114.86
24	7510656.56	4693490.31	648.18	perdhese-terasa			
<b>Gjithsej:</b>							<b>114.86</b>

Nr.	Y	X	H	D	Etazhi	Sqarim	Sipërfaqja (m <sup>2</sup> )
47	7510657.78	4693488.79	651.39	kati1	Kati 1	Kati 1	77.70
48	7510657.56	4693488.66	651.39	kati1			
49	7510650.67	4693484.47	651.39	kati1			
56	7510662.60	4693480.53	651.39	kati1			
57	7510658.73	4693478.03	651.39	kati1			
58	7510656.99	4693476.97	651.39	kati1			
73	7510658.66	4693478.14	651.39	kati1			
74	7510655.12	4693477.12	651.39	kati1			
87	7510656.43	4693477.92	651.39	kati1			
45	7510650.10	4693485.42	651.39	kati1 terasa			
46	7510657.02	4693489.55	651.39	kati1 terasa			
<b>Gjithsej:</b>							<b>86.36</b>

Nr.	Y	X	H	D	Etazhi	Sqarim	Sipërfaqja (m <sup>2</sup> )
12	7510650.66	4693484.49	645.94	bodrum	Bodrumi	Bodrumi	50.09
13	7510657.12	4693488.34	645.94	bodrum			
14	7510657.07	4693488.41	646.09	bodrum			
17	7510659.76	4693489.99	645.94	bodrum			
18	7510662.16	4693485.87	645.94	bodrum	Gjithsej:	50.09	50.09
117	7510653.07	4693480.46	645.94	bodrum			

Gjeodeti / Kompania gjeodete e licencuar:	Liridon Sejdiu	Nënshkrimi dhe vula:
Numri i licencës	140	

**Republika e Kosovës**

Republika Kosova-Republic of Kosovo


Qeveria -Vlada-Government

Ministria e Mjedisit dhe Planifikimit Hapësinor /Ministarstvo Sredine i Prostornog Planiranja/Ministry of Environment and Spatial Planning

AGJENCIA KADASTRALE E KOSOVËS/KATASTARSKA AGENCIJA KOSOVA/KOSOVA CADASTRAL AGENCY



Nr	Y	X	H	Kodi	Përshkrimi	Burimi
25	7510662.596	4693480.525	648.248	40	Shtëpi-Ndërtesë	PM
26	7510659.761	4693489.987	648.248	40	Shtëpi-Ndërtesë	PM
27	7510662.412	4693480.841	648.248	40	Shtëpi-Ndërtesë	PM
28	7510657.565	4693488.655	648.248	40	Shtëpi-Ndërtesë	PM
29	7510664.392	4693482.042	648.248	40	Shtëpi-Ndërtesë	PM
30	7510650.670	4693484.474	648.248	40	Shtëpi-Ndërtesë	PM
109	7510658.660	4693478.138	648.248	40	Shtëpi-Ndërtesë	PM
110	7510658.725	4693478.027	648.248	40	Shtëpi-Ndërtesë	PM
111	7510656.985	4693476.971	648.248	40	Shtëpi-Ndërtesë	PM
112	7510656.434	4693477.917	648.248	40	Shtëpi-Ndërtesë	PM
113	7510655.087	4693477.101	648.248	40	Shtëpi-Ndërtesë	PM
23	7510649.643	4693486.188	648.248	40	Shtëpi-Ndërtesë	PM
24	7510656.560	4693490.312	648.181	40	Shtëpi-Ndërtesë	PM

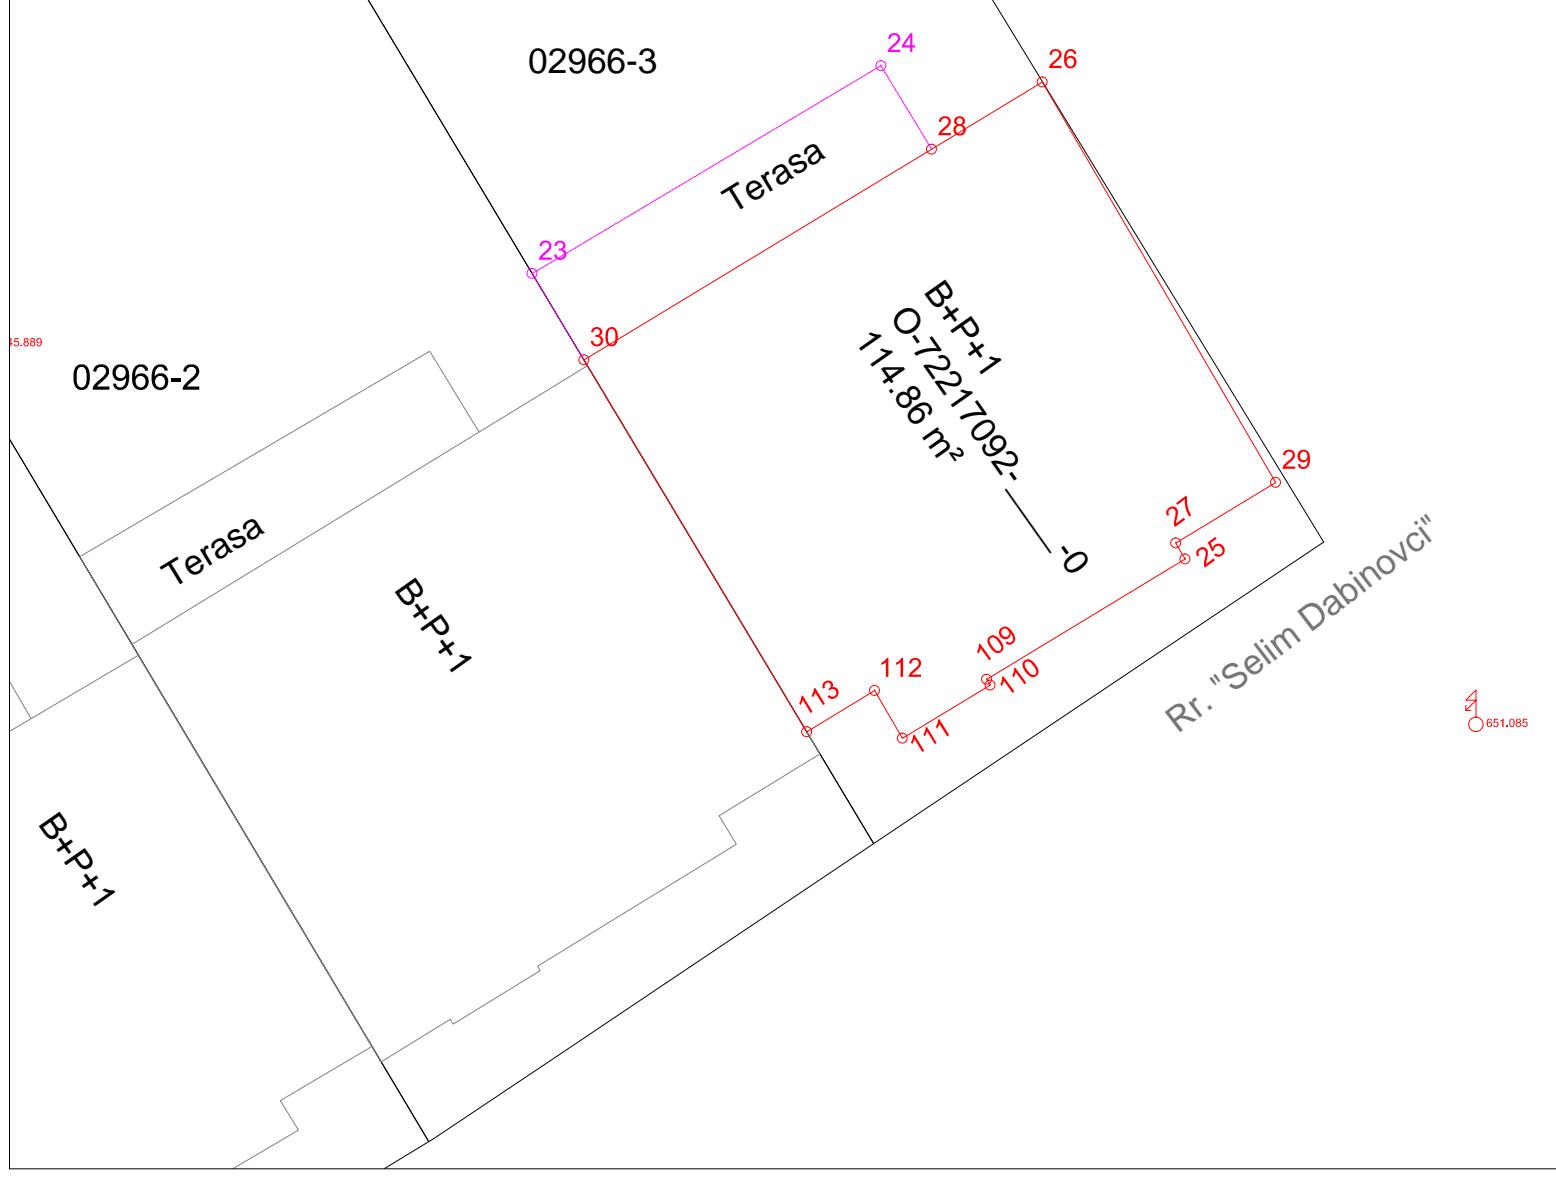Rilevoi / Snimio: LIRIDON SEJDIU  
(emri dhe mbiemri i gjyqetarit/kompanisë/ ime i prezime geodeta/ kompanije)Nr. i licencës / Br. licence: 140

V.V.

Nënshkrimi / Potpis: \_\_\_\_\_

Aprovoi / Usvojio: \_\_\_\_\_  
(emri dhe mbiemri i pësonit zyrtar/ ime i prezime sluzbeneg lica)Data e rilevimit / Datum snimanja: 19.07.2025

Data e rilevimit / Datum snimanja: \_\_\_\_\_



Republika e Kosovës  
Republika Kosova-Republic of Kosovo  
Qeveria e Kosovës- Vlada Kosova- Government of Kosovo  
Ministria e Infrastrukturës dhe Ambientit/ Ministrastvo Infrastrukture i Sredine/ Ministry of Infrastructure and Environment  
AGJENCIA KADASTRALE E KOSOVËS/KOSOVSKA KATASTARSKA AGENCIJA/ KOSOVO CADASTRAL AGENCY

<b>Komuna:</b> Ferizaj	<b>Zona Kadastrale:</b> Ferizaj
<b>Numri i njësis kadastrale:</b> 02966-3	<b>Sistemi koordinat:</b> KosovaRef01

Nr	Y	X	H	Kodi	Përshkrimi	Burimi
25	7510662.596	4693480.525	648.248	40	Shtëpi-Ndërtesë	PM
26	7510659.761	4693489.987	648.248	40	Shtëpi-Ndërtesë	PM
27	7510662.412	4693480.841	648.248	40	Shtëpi-Ndërtesë	PM
28	7510657.565	4693488.655	648.248	40	Shtëpi-Ndërtesë	PM
29	7510664.392	4693482.042	648.248	40	Shtëpi-Ndërtesë	PM
30	7510650.670	4693484.474	648.248	40	Shtëpi-Ndërtesë	PM
109	7510658.660	4693478.138	648.248	40	Shtëpi-Ndërtesë	PM
110	7510658.725	4693478.027	648.248	40	Shtëpi-Ndërtesë	PM
111	7510656.985	4693476.971	648.248	40	Shtëpi-Ndërtesë	PM
112	7510656.434	4693477.917	648.248	40	Shtëpi-Ndërtesë	PM
113	7510655.087	4693477.101	648.248	40	Shtëpi-Ndërtesë	PM
23	7510649.643	4693486.188	648.248	40	Shtëpi-Ndërtesë	PM
24	7510656.560	4693490.312	648.181	40	Shtëpi-Ndërtesë	PM

Gjeodeti / Kompania gjeodete e licencuar:	Liridon Sejdiu	Nënshkrimi dhe vula:	
Numri i licencës	140		



Republika e Kosovës

Republika Kosova - Republic of Kosovo

Qeveria e Kosovës - Vlada Kosova - Government of Kosovo

Ministria e Infrastrukturës dhe Ambientit/ Ministrastvo Infrastrukture i Sredine/ Ministry of Infrastructure and Environment

AGJENCIA KADASTRALE E KOSOVËS/ KOSOVSKA KATASTARSKA AGENCIJA/ KOSOVA CADASTRAL AGENCY

R E G J I S T R I M I I N DERTESËS / SHTËPISË													
Nr	Komuna	Zona Kadastrale	Numri i ndërtesës (njësia)	Etazhiteti	Katet	Sipërfaqja e kateve [m <sup>2</sup> ]	Sipërfaqja e bazamentit [m <sup>2</sup> ]	Adresa e Njësisë	Vendi i quajtur	Shfrytëzimi i aktual	Pronari / Shfrytëzuesi Emri (Emri i prindit) Mbiemri	Numri përsoneal	Pjesa e Pronës
1	Ferizaj	Ferizaj	O-72217092-_____0	B+P+1	Bodrumi	50.09	99	Rr. "Selim Dabinovci"- Ferizaj	KODRA E KAZERMËS	Banim	Armend (Habil) Dabinovci	1005004957	1/1
					Përdhesa	114.86							
					Kati 1	86.36							
					Gjithsej:	251.31							

Gjeodeti/kompania e licencuar: LIRIDON SEJDIU

Nr i licencës: 140

Nënshkrimi dhe vula:

















