


Nr	Y	X	H	Kodi	Përshtkimi	Burimi
31	7510650.738	4693484.360	648.248	40	Shtëpi-Ndërtesë	PM
32	7510653.353	4693475.437	648.248	40	Shtëpi-Ndërtesë	PM
33	7510655.351	4693476.659	648.248	40	Shtëpi-Ndërtesë	PM
34	7510648.589	4693483.046	648.248	40	Shtëpi-Ndërtesë	PM
35	7510641.701	4693478.833	648.248	40	Shtëpi-Ndërtesë	PM
103	7510653.694	4693474.867	648.248	40	Shtëpi-Ndërtesë	PM
104	7510649.748	4693472.454	648.248	40	Shtëpi-Ndërtesë	PM
105	7510649.804	4693472.359	648.248	40	Shtëpi-Ndërtesë	PM
106	7510648.074	4693471.301	648.248	40	Shtëpi-Ndërtesë	PM
107	7510648.018	4693471.396	648.248	40	Shtëpi-Ndërtesë	PM
108	7510646.643	4693470.555	648.248	40	Shtëpi-Ndërtesë	PM
21	7510640.665	4693480.568	648.248	40	Shtëpi-Ndërtesë	PM
22	7510647.612	4693484.644	648.253	40	Shtëpi-Ndërtesë	PM

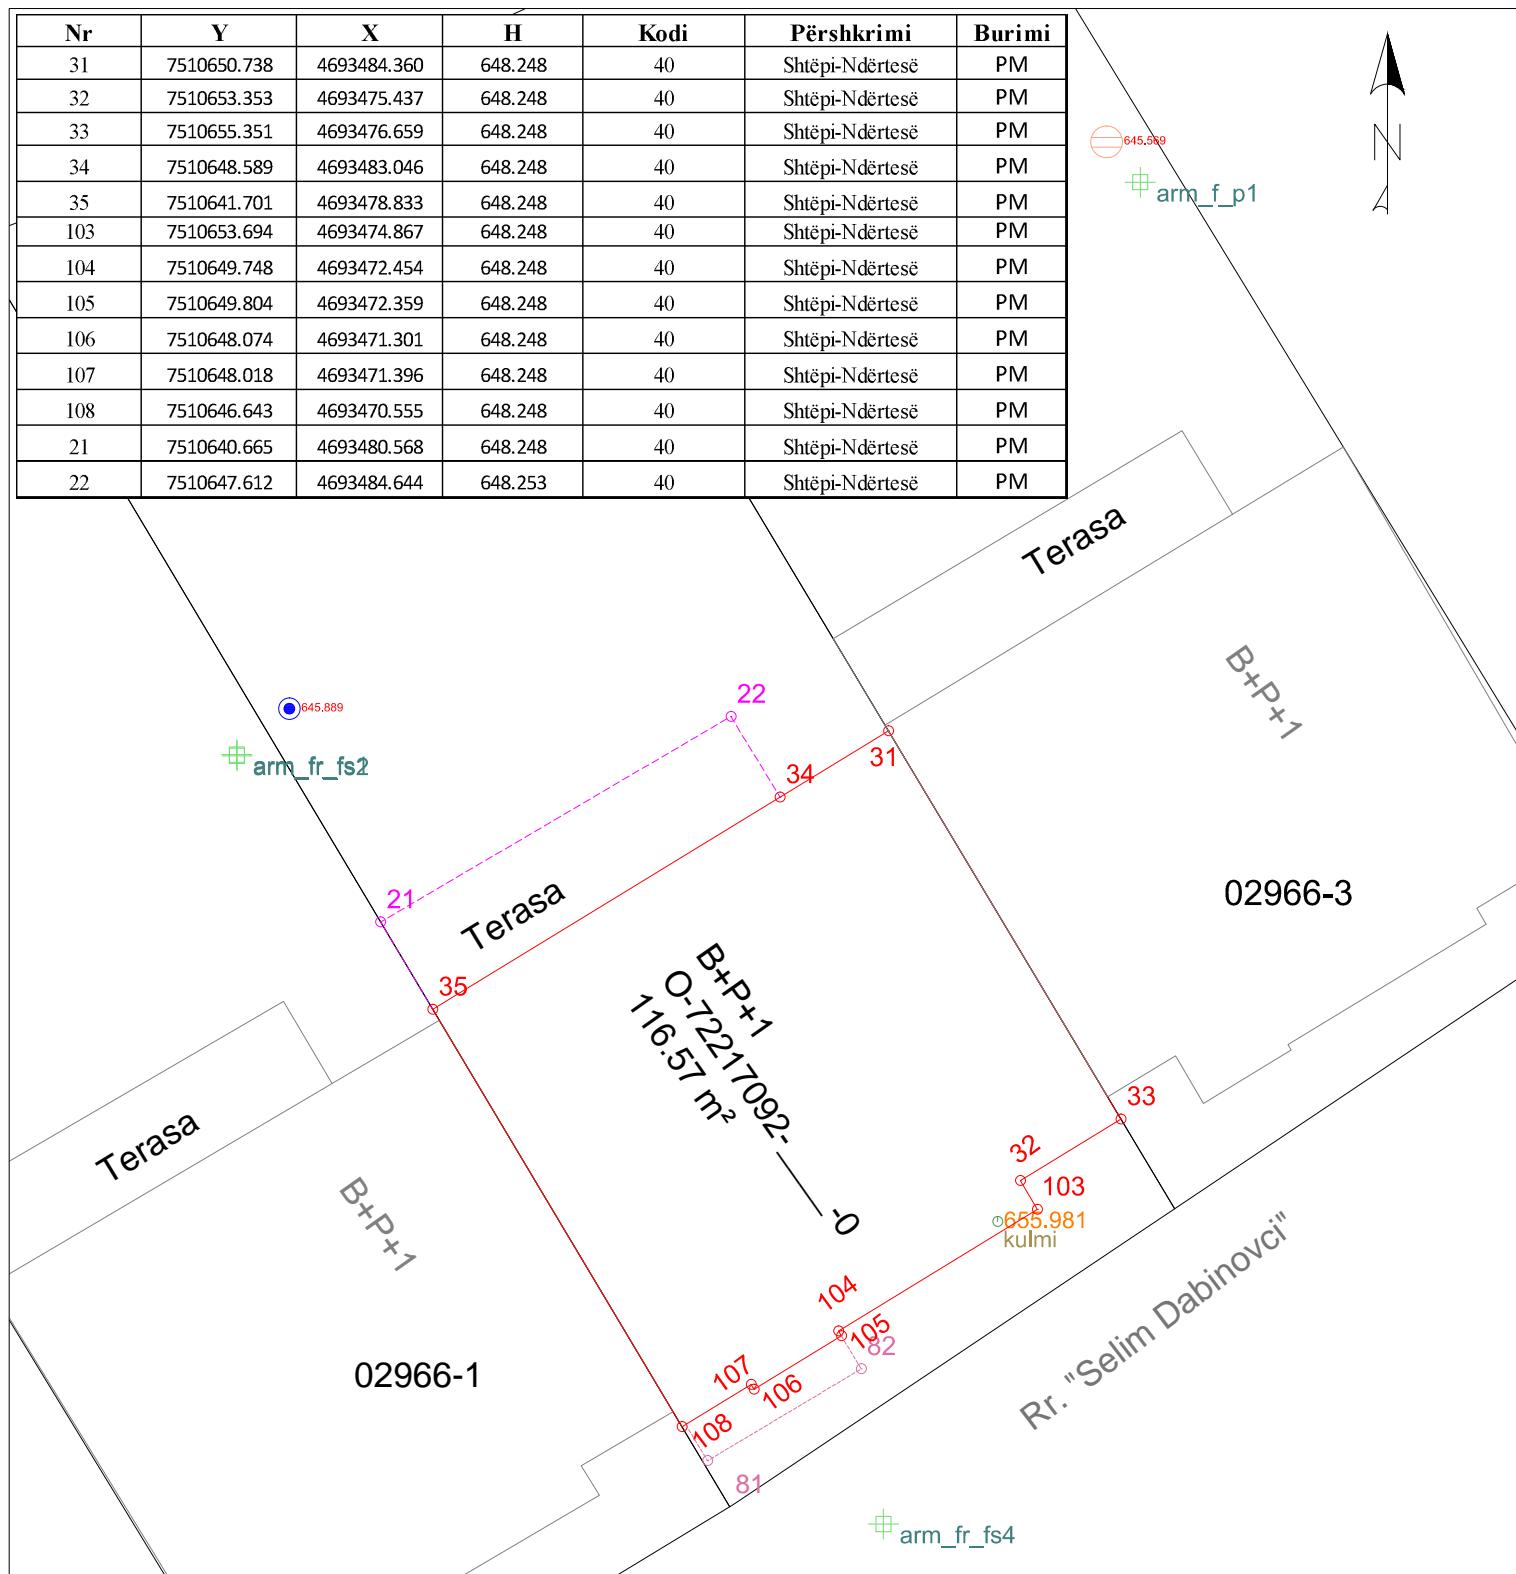

### Situacioni i terrenit

Zyra kadastrale kmunale / pëtinska katastarska kancelarija: Ferizaj

Zona kadastrale / Katastarska zona: Ferizaj

Nr. i njësisë kadastrale / Br. katastarske jedinice : 02966-2

Numri i lëndës / Broj predmeta:

Shkalla e zvoglimit / Razmera plana 1: 150


### Lista e koordinatave të pikave të matura:

Nr	Y	X	H	DSC
88	7510622.908	4693458.842	646.236	ard_fr_p2
89	7510600.989	4693466.253	642.582	ard_fr_p3
90	7510642.920	4693459.301	651.363	ard_fr_p4
91	7510657.311	4693459.617	651.229	ard_fr_p5
92	7510675.977	4693474.073	651.220	ard_fr_p6
93	7510655.734	4693495.242	645.569	arm_f_p1
94	7510637.813	4693483.888	646.943	arm_fr_fs1
95	7510637.817	4693483.863	646.969	arm_fr_fs2
96	7510650.640	4693468.626	653.133	arm_fr_fs4
76	7510652.907	4693474.628	655.981	kulmi
97	7510638.853	4693484.798	645.889	kyqje-uj
31	7510650.738	4693484.360	648.248	perdhese
32	7510653.353	4693475.437	648.248	perdhese
33	7510655.351	4693476.659	648.248	perdhese
34	7510648.589	4693483.046	648.248	perdhese
35	7510641.701	4693478.833	648.248	perdhese
103	7510653.694	4693474.867	648.248	perdhese
104	7510649.748	4693472.454	648.248	perdhese
105	7510649.8	4693472.359	648.248	perdhese
106	7510648.074	4693471.301	648.248	perdhese
107	7510640.665	4693480.568	648.248	perdhese
108	7510647.612	4693484.644	648.253	perdhese
21	7510640.66	4693480.55	648.248	perdhese-terasa
22	7510647.61	4693484.64	648.253	perdhese-terasa
353	7510655.06	4693496.04	645.569	pusetEkele
1	7510668.36	4693477.25	651.085	shtyElektrike
81	7510647.15	4693469.88	654.327	streha
82	7510650.2	4693471.7	654.34	streha

### Shpjegues:

- Kufiri kadastral (nga SIKTK-G)
- Ndërtesa në trajtim për legalizim
- Ndërtesa tjera
- Aneks Ndërtimi
- ▲ Shtyllë elektrike
- Pusetë e ujësjellësit
- Pusetë e ujërave të zeza
- Strehët
- ④ Kyqje në rrymë
- Rilevoi / Snimi: LIRIDON SEJDIU  
(emri dhe mbiemri i gjedjetit/kompanisë / ime i prezime gedeta/ kompanije)
- Nr. i licencës / Br. licence: 140
- Data e rilevimit / Datum snimanja: 19.07.2025
- Nënshkrimi / Potpis: \_\_\_\_\_  
V.V.

Nr	Y	X	H	Kodi	Përshtkimi	Burimi
31	7510650.738	4693484.360	648.248	40	Shtëpi-Ndërtesë	PM
32	7510653.353	4693475.437	648.248	40	Shtëpi-Ndërtesë	PM
33	7510655.351	4693476.659	648.248	40	Shtëpi-Ndërtesë	PM
34	7510648.589	4693483.046	648.248	40	Shtëpi-Ndërtesë	PM
35	7510641.701	4693478.833	648.248	40	Shtëpi-Ndërtesë	PM
103	7510653.694	4693474.867	648.248	40	Shtëpi-Ndërtesë	PM
104	7510649.748	4693472.454	648.248	40	Shtëpi-Ndërtesë	PM
105	7510649.804	4693472.359	648.248	40	Shtëpi-Ndërtesë	PM
106	7510648.074	4693471.301	648.248	40	Shtëpi-Ndërtesë	PM
107	7510648.018	4693471.396	648.248	40	Shtëpi-Ndërtesë	PM
108	7510646.643	4693470.555	648.248	40	Shtëpi-Ndërtesë	PM
21	7510640.665	4693480.568	648.248	40	Shtëpi-Ndërtesë	PM
22	7510647.612	4693484.644	648.253	40	Shtëpi-Ndërtesë	PM

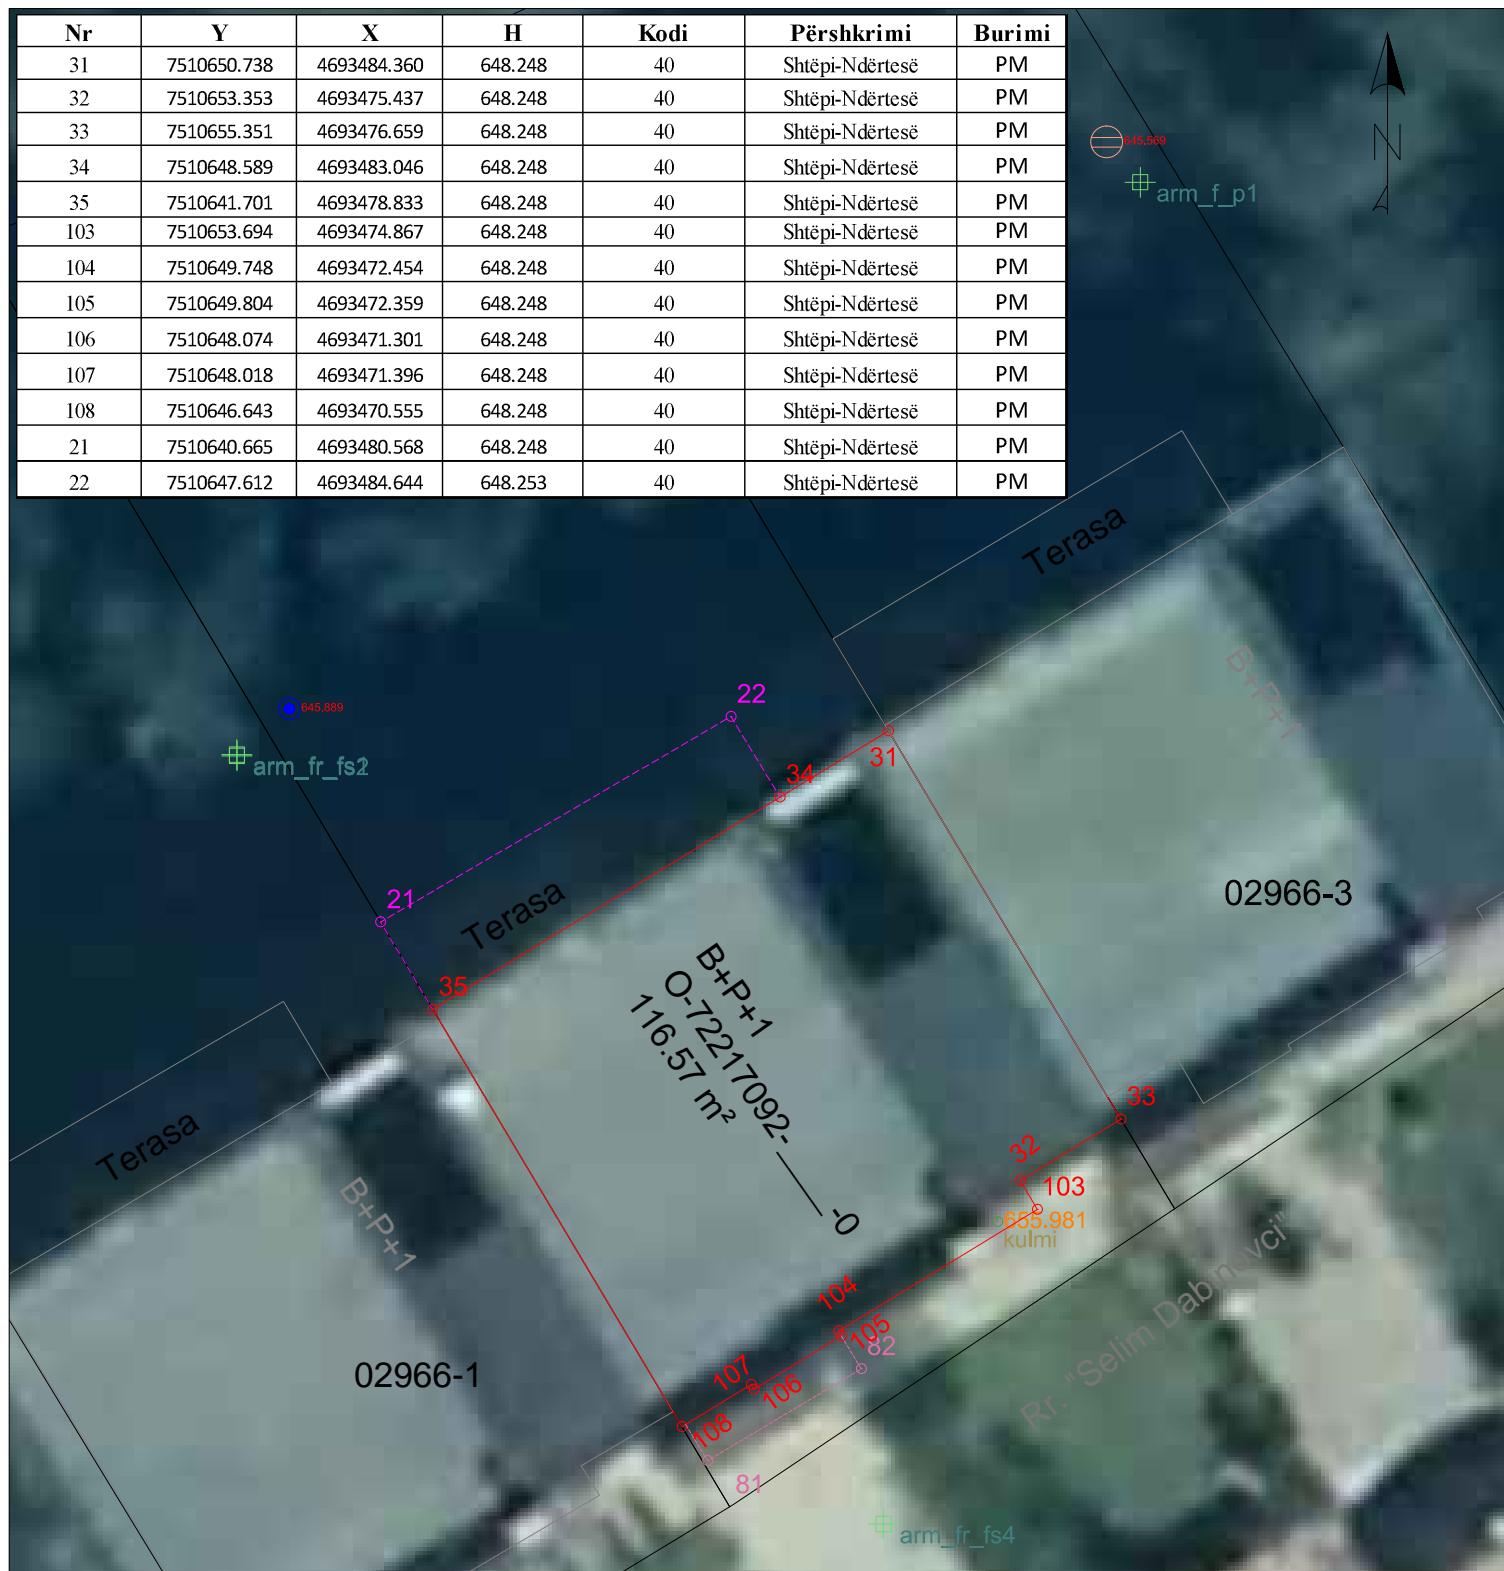



Republika e Kosovës  
Republika Kosova-Republic of Kosovo  
Qeveria e Kosovës- Vlada Kosova- Government of Kosovo  
Ministria e Infrastrukturës dhe Ambientit/ Ministrastvo Infrastrukture i Sredine/ Ministry of Infrastructure and Environment  
AGJENCIA KADASTRALE E KOSOVËS/KOSOVSKA KATASTARSKA AGENCIJA/ KOSOVO CADASTRAL AGENCY

<b>Komuna:</b> Ferizaj	<b>Zona Kadastrale:</b> Ferizaj
<b>Numri i njësis kadastrale:</b> 02966-2	<b>Sistemi koordinat:</b> KosovaRef01

Nr	Y	X	H	Kodi	Përshkrimi	Burimi
31	7510650.738	4693484.360	648.248	40	Shtëpi-Ndërtesë	PM
32	7510653.353	4693475.437	648.248	40	Shtëpi-Ndërtesë	PM
33	7510655.351	4693476.659	648.248	40	Shtëpi-Ndërtesë	PM
34	7510648.589	4693483.046	648.248	40	Shtëpi-Ndërtesë	PM
35	7510641.701	4693478.833	648.248	40	Shtëpi-Ndërtesë	PM
103	7510653.694	4693474.867	648.248	40	Shtëpi-Ndërtesë	PM
104	7510649.748	4693472.454	648.248	40	Shtëpi-Ndërtesë	PM
105	7510649.804	4693472.359	648.248	40	Shtëpi-Ndërtesë	PM
106	7510648.074	4693471.301	648.248	40	Shtëpi-Ndërtesë	PM
107	7510648.018	4693471.396	648.248	40	Shtëpi-Ndërtesë	PM
108	7510646.643	4693470.555	648.248	40	Shtëpi-Ndërtesë	PM
21	7510640.665	4693480.568	648.248	40	Shtëpi-Ndërtesë	PM
22	7510647.612	4693484.644	648.253	40	Shtëpi-Ndërtesë	PM

Gjeodeti / Kompania gjeodete e licencuar:	Liridon Sejdiu	Nënshkrimi dhe vula:	
Numri i licencës	140		

Kérko Rezultati i kérkimit

Shfaq Zgjedhur Rezultatet Shkarko

ParcelDetailId	CadastreUnitId	CadastreZoneId	Ca
11160174	P-72217092-02...	72217092	72

Vendos në objekt Zmadho në objekt

Numri i rezultateve: 1 (showing first 1)  
Nga harta: 0

**Detajet**

ParcelDetailId:	11160174
CadastreUnitId:	P-72217092-02966-2
CadastreZoneId:	72217092
CadastreZoneCode:	72217092
Geometry:	
Status:	1
Sipërfaqja Grafike (m <sup>2</sup> ):	298.0

Rapor

**Lista e shtresës** Ndhima

- Ortofoto
  - Orthophoto2024Rural
  - Orthophoto2024Urban
  - Orthophoto2018Rural
  - Orthophoto2018Malore
  - Orthophoto2018Urban
  - Orthofoto 2015 UAV
  - Orthofoto 2012
  - Orthofoto 2009
  - Orthofoto 2004
- Hartat Topografike
  - Harta Topografike 1:250000
  - Harta Topografike 1:25000 (2015)
  - Nomenklatura
- Rindertimi i Informacioneve Kadastrale
  - RIK\_2025
- Modeli Dixhital i Terrenit
  - Modeli Dixhital i Terrenit
- Rilevimi
  - Indexi i Ortofotove Rurale 2024
  - Indexi i Ortofotove Urbane 202
  - Indeksi i Ortofotove 2018
- Rrjeti Rugor
  - Autostradë
  - Rrugë Nacionale
  - Rrugë Rajonale
- Njësi Administrative
  - Kufiri Shtetëror
  - Kufijë dhe Emrat e Komunave
  - Zonë urbane
- Njësítë Kadastrale
  - Zonat Kadastrale
  - Parcelat
  - Numri parcelës
  - Ndërtesarat
  - Numri ndërtësës
- Sistemi i Adresave
  - Rrugët

1 : 250 Auto Shfaq këshillat Kérko

SELIM DABINOVCI

Scale = 1 : 250

Pozita: 7510641.114, 4693489.382

KosovaRef01

Zyra kadastrale komunale / Opštinska katastarska kancelarija: FerizajNr. i njësisë kadastrale / Br. katastarske jedinice : 02966-2Zona kadastrale / Katastarska zona: Ferizaj

Numri i lëndës / Broj predmeta: \_\_\_\_\_

Lloji i njësisë kadastrale / Vrsta katastarske jedinice : ShtëpiShkalla e zvoglimit / Razmera plana 1: 150**Republika e Kosovës**

Republika Kosova-Republic of Kosovo

Qeveria -Vlada-Government

Ministria e Mjedisit dhe Planifikimit Hapësinor /Ministarstvo Sredine i Prostornog Planiranja/Ministry of Environment and Spatial Planning

AGJENCIA KADASTRALE E KOSOVËS/KATASTARSKA AGECIJA KOSOVA/KOSOVA CADASTRAL AGENCY

**02966-2****Terasa****02966-3****Terasa****B+P+1****02966-1****Bodrumi  
O-72217092-  
50.45 m<sup>2</sup>****115****7****8****9****118****119****124****116****Rr. "Selim Dabinovci"**

Nr.	Y	X	H	D	Etazhi	Sqarim	Sipërfaqja (m <sup>2</sup> )
7	7510641.69	4693478.87	645.97	bodrum	Bodrumi	Bodrumi	50.45
8	7510648.11	4693482.65	645.94	bodrum			
9	7510648.06	4693482.74	645.86	bodrum			
115	7510644.09	4693474.83	645.94	bodrum			
116	7510653.22	4693480.21	645.94	bodrum			
118	7510648.58	4693483.20	645.94	bodrum			
119	7510648.64	4693483.08	645.94	bodrum			
124	7510650.69	4693484.44	645.94	bodrum		Gjithsej:	50.45

Rilevoi / Snimio: LIRIDON SEJDIU  
(emri dhe mbiemri i gjyqetarit/kompanisë / ime i prezime geodeta/ kompanije)Aprovoi / Usvojio: \_\_\_\_\_  
(emri dhe mbiemri i pësonit zyrtar/ ime i prezime sluzbeneg lica)Nr. i licencës / Br. licence: 140

V.V.

Nënshkrimi / Potpis: \_\_\_\_\_

Nënshkrimi / Potpis: \_\_\_\_\_

Data e rilevimit / Datum snimanja: 18.03.2024

Data e rilevimit / Datum snimanja: \_\_\_\_\_



## Republika e Kosovës

Republika Kosova-Republic of Kosovo

Qeveria -Vlada-Government

Ministria e Mjedisit dhe Planifikimit Hapësinor /Ministarstvo Sredine i Prostornog Planiranja/Ministry of Environment and Spatial Planning

AGJENCIA KADASTRALE E KOSOVËS/KATASTARSKA AGECIJA KOSOVA/KOSOVA CADASTRAL AGENCY



02966-2

Përdhesa  
O-12217092-  
116.57 m<sup>2</sup>

Terasa

02966-1

Rr. "Selim Dabinovci"

02966-3

B+P+1

B+P+1



Nr.	Y	X	H	D	Etazi	Sqarim	Sipërfaqja (m <sup>2</sup> )
31	7510650.74	4693484.36	648.25	perdhese	Përdhesa	Përdhesa	100.87
32	7510653.35	4693475.44	648.25	perdhese			
33	7510655.35	4693476.66	648.25	perdhese			
34	7510648.59	4693483.05	648.25	perdhese			
35	7510641.70	4693478.83	648.25	perdhese			
103	7510653.69	4693474.87	648.25	perdhese			
104	7510649.75	4693472.45	648.25	perdhese			
105	7510649.80	4693472.36	648.25	perdhese			
106	7510648.07	4693471.30	648.25	perdhese			
107	7510648.02	4693471.40	648.25	perdhese			
108	7510646.64	4693470.55	648.25	perdhese	Terasa	15.70	116.57
21	7510640.66	4693480.57	648.25	perdhese-terasa			
22	7510647.61	4693484.64	648.25	perdhese-terasa			
				Gjithsej:			

Rilevoi / Snimio: LIRIDON SEJDIU  
(emri dhe mbiemri i gjykozit/kompanisë/ ime i prezime geodeta/ kompanije)Aprovoi / Usvojio: \_\_\_\_\_  
(emri dhe mbiemri i pësonit zyrtar/ ime i prezime sluzbeneg lica)

Nr. i licencës / Br. licence: 140

V.V.

Nënshkrimi / Potpis: \_\_\_\_\_

Nënshkrimi / Potpis: \_\_\_\_\_

Data e rilevimit / Datum snimanja: 18.03.2024

Data e rilevimit / Datum snimanja: \_\_\_\_\_

Zyra kadastrale komunale / Opštinska katastarska kancelarija: FerizajNr. i njësisë kadastrale / Br. katastarske jedinice : 02966-2Zona kadastrale / Katastarska zona: Ferizaj

Numri i lëndës / Broj predmeta: \_\_\_\_\_

Lloji i njësisë kadastrale / Vrsta katastarske jedinice : ShtëpiShkalla e zvoglimit / Razmera plana 1: 150**Republika e Kosovës**

Republika Kosova-Republic of Kosovo

Qeveria -Vlada-Government

Ministria e Mjedisit dhe Planifikimit Hapësinor /Ministarstvo Sredine i Prostornog Planiranja/Ministry of Environment and Spatial Planning

AGJENCIA KADASTRALE E KOSOVËS/KATASTARSKA AGECIJA KOSOVA/KOSOVA CADASTRAL AGENCY



Nr.	Y	X	H	D	Etazhi	Sqarim	Sipërfaqja (m <sup>2</sup> )
50	7510648.74	4693483.14	651.39	katil	Kati 1	Kati 1	79.84
51	7510648.59	4693483.05	651.39	katil			
52	7510641.70	4693478.83	651.39	katil			
60	7510653.69	4693474.87	651.39	katil			
61	7510649.80	4693472.36	651.39	katil			
62	7510648.07	4693471.32	651.39	katil			
63	7510648.02	4693471.40	651.39	katil			
64	7510646.64	4693470.55	651.39	katil			
75	7510649.75	4693472.45	651.39	katil			
43	7510641.13	4693479.78	651.39	katil terasa			
44	7510648.09	4693483.86	651.39	katil terasa		Gjithsej:	88.16

Rilevoi / Snimio: LIRIDON SEJDIU  
(emri dhe mbiemri i gjydetit/kompanisë/ ime i prezime geodeta/ kompanije)Aprovoi / Usvojio: \_\_\_\_\_  
(emri dhe mbiemri i pësonit zyrtar/ ime i prezime sluzbeneg lica)Nr. i licencës / Br. licence: 140

V.V.

Nënshkrimi / Potpis: \_\_\_\_\_

Nënshkrimi / Potpis: \_\_\_\_\_

Data e rilevimit / Datum snimanja: 18.03.2024

Data e rilevimit / Datum snimanja: \_\_\_\_\_



Republika e Kosovës

Republika Kosova-Republic of Kosovo

Geveria e Kosovës- Vlada Kosova- Government of Kosovo

Ministria e Infrastrukturës dhe Ambientit/ Ministrastvo Infrastrukture i Sredine/ Ministry of Infrastructure and Environment

AGJENCIA KADASTRALE E KOSOVËS/KOSOVSKA KATASTARSKA AGENCIJA/ KOSOVO CADASTRAL AGENCY

**Komuna: Ferizaj**  
**Numri i njësis kadastrale: 02966-2**


**Zona Kadastrale: Ferizaj**  
**Sistemi koordinat: KosovaRef01**

Nr.	Y	X	H	D	Etazhi	Sqarim	Sipërfaqja (m <sup>2</sup> )
31	7510650.74	4693484.36	648.25	perdhese	Përdhesa		100.87
32	7510653.35	4693475.44	648.25	perdhese			
33	7510655.35	4693476.66	648.25	perdhese			
34	7510648.59	4693483.05	648.25	perdhese			
35	7510641.70	4693478.83	648.25	perdhese			
103	7510653.69	4693474.87	648.25	perdhese			
104	7510649.75	4693472.45	648.25	perdhese			
105	7510649.80	4693472.36	648.25	perdhese			
106	7510648.07	4693471.30	648.25	perdhese			
107	7510648.02	4693471.40	648.25	perdhese			
108	7510646.64	4693470.55	648.25	perdhese	Terasa		15.70
21	7510640.66	4693480.57	648.25	perdhese-terasa			
22	7510647.61	4693484.64	648.25	perdhese-terasa	Gjithsej:		116.57

Nr.	Y	X	H	D	Etazhi	Sqarim	Sipërfaqja (m <sup>2</sup> )
50	7510648.74	4693483.14	651.39	kati1	Kati 1		79.84
51	7510648.59	4693483.05	651.39	kati1			
52	7510641.70	4693478.83	651.39	kati1			
60	7510653.69	4693474.87	651.39	kati1			
61	7510649.80	4693472.36	651.39	kati1			
62	7510648.07	4693471.32	651.39	kati1			
63	7510648.02	4693471.40	651.39	kati1			
64	7510646.64	4693470.55	651.39	kati1			
75	7510649.75	4693472.45	651.39	kati1			
43	7510641.13	4693479.78	651.39	kati1 terasa			
44	7510648.09	4693483.86	651.39	kati1 terasa	Gjithsej:		88.16

Nr.	Y	X	H	D	Etazhi	Sqarim	Sipërfaqja (m <sup>2</sup> )
7	7510641.69	4693478.87	645.97	bodrum	Bodrumi		50.45
8	7510648.11	4693482.65	645.94	bodrum			
9	7510648.06	4693482.74	645.86	bodrum			
115	7510644.09	4693474.83	645.94	bodrum			
116	7510653.22	4693480.21	645.94	bodrum			
118	7510648.58	4693483.20	645.94	bodrum			
119	7510648.64	4693483.08	645.94	bodrum			
124	7510650.69	4693484.44	645.94	bodrum			

Gjeodeti / Kompania gjeodete e licencuar:	Liridon Sejdiu	Nënshkrimi dhe vula:	
Numri i licencës	140		

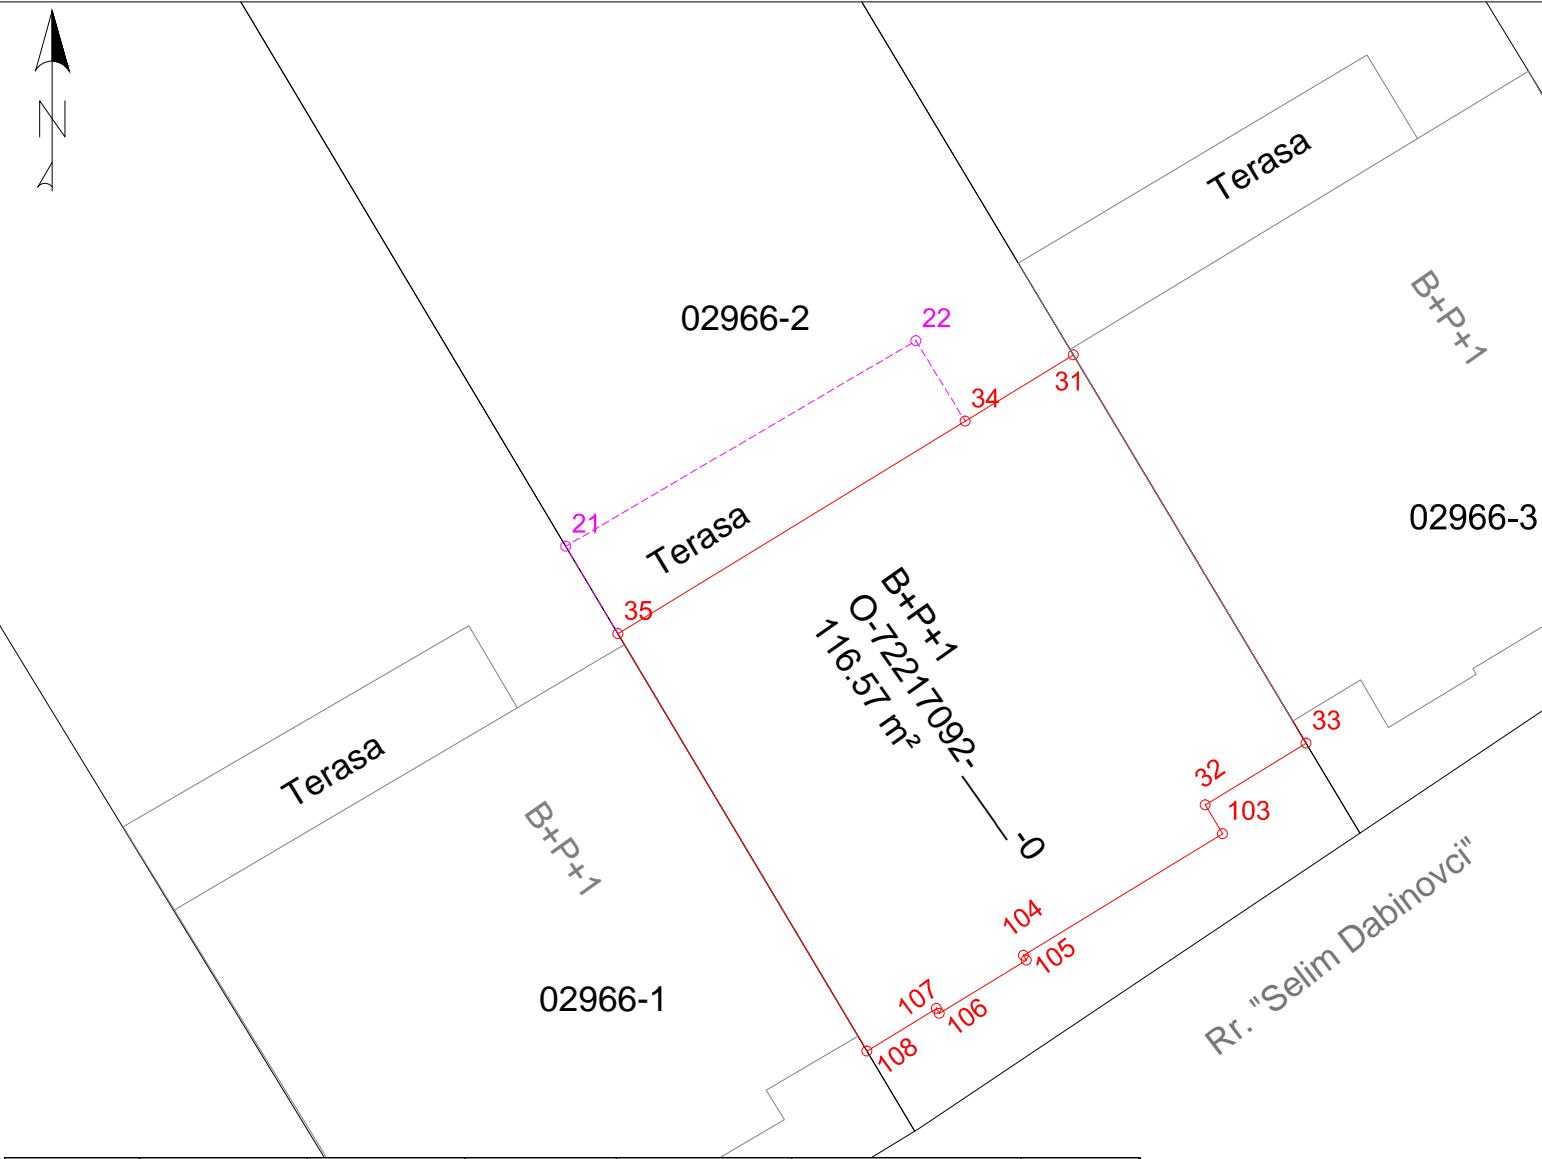

Nr	Y	X	H	Kodi	Përvetimi	Burimi
31	7510650.738	4693484.360	648.248	40	Shtëpi-Ndërtesë	PM
32	7510653.353	4693475.437	648.248	40	Shtëpi-Ndërtesë	PM
33	7510655.351	4693476.659	648.248	40	Shtëpi-Ndërtesë	PM
34	7510648.589	4693483.046	648.248	40	Shtëpi-Ndërtesë	PM
35	7510641.701	4693478.833	648.248	40	Shtëpi-Ndërtesë	PM
103	7510653.694	4693474.867	648.248	40	Shtëpi-Ndërtesë	PM
104	7510649.748	4693472.454	648.248	40	Shtëpi-Ndërtesë	PM
105	7510649.804	4693472.359	648.248	40	Shtëpi-Ndërtesë	PM
106	7510648.074	4693471.301	648.248	40	Shtëpi-Ndërtesë	PM
107	7510648.018	4693471.396	648.248	40	Shtëpi-Ndërtesë	PM
108	7510646.643	4693470.555	648.248	40	Shtëpi-Ndërtesë	PM
21	7510640.665	4693480.568	648.248	40	Shtëpi-Ndërtesë	PM
22	7510647.612	4693484.644	648.253	40	Shtëpi-Ndërtesë	PM

Rilevoi / Snimio: LIRIDON SEJDIU  
(emri dhe mbiemri i gjyqat/kompanisë/ ime i prezime geodeta/ kompanije)Aprovoi / Usvojo: \_\_\_\_\_  
(emri dhe mbiemri i pësonit zyrtar/ ime i prezime sluzbeneg lica)

Nr. i licencës / Br. licence: 140

V.V.

Nënshkrimi / Potpis: \_\_\_\_\_

Nënshkrimi / Potpis: \_\_\_\_\_

Data e rilevimit / Datum snimanja: 18.03.2024

Data e rilevimit / Datum snimanja: \_\_\_\_\_



Republika e Kosovës  
Republika Kosova-Republic of Kosovo  
Qeveria e Kosovës- Vlada Kosova- Government of Kosovo  
Ministria e Infrastrukturës dhe Ambientit/ Ministrastvo Infrastrukture i Sredine/ Ministry of Infrastructure and Environment  
AGJENCIA KADASTRALE E KOSOVËS/KOSOVSKA KATASTARSKA AGENCIJA/ KOSOVO CADASTRAL AGENCY

<b>Komuna:</b> Ferizaj	<b>Zona Kadastrale:</b> Ferizaj
<b>Numri i njësis kadastrale:</b> 02966-2	<b>Sistemi koordinat:</b> KosovaRef01

Nr	Y	X	H	Kodi	Përshkrimi	Burimi
31	7510650.738	4693484.360	648.248	40	Shtëpi-Ndërtesë	PM
32	7510653.353	4693475.437	648.248	40	Shtëpi-Ndërtesë	PM
33	7510655.351	4693476.659	648.248	40	Shtëpi-Ndërtesë	PM
34	7510648.589	4693483.046	648.248	40	Shtëpi-Ndërtesë	PM
35	7510641.701	4693478.833	648.248	40	Shtëpi-Ndërtesë	PM
103	7510653.694	4693474.867	648.248	40	Shtëpi-Ndërtesë	PM
104	7510649.748	4693472.454	648.248	40	Shtëpi-Ndërtesë	PM
105	7510649.804	4693472.359	648.248	40	Shtëpi-Ndërtesë	PM
106	7510648.074	4693471.301	648.248	40	Shtëpi-Ndërtesë	PM
107	7510648.018	4693471.396	648.248	40	Shtëpi-Ndërtesë	PM
108	7510646.643	4693470.555	648.248	40	Shtëpi-Ndërtesë	PM
21	7510640.665	4693480.568	648.248	40	Shtëpi-Ndërtesë	PM
22	7510647.612	4693484.644	648.253	40	Shtëpi-Ndërtesë	PM

Gjeodeti / Kompania gjeodete e licencuar:	Liridon Sejdiu	Nënshkrimi dhe vula:	
Numri i licencës	140		



Republika e Kosovës

Republika Kosova - Republic of Kosovo

Qeveria e Kosovës - Vlada Kosova - Government of Kosovo

Ministria e Infrastrukturës dhe Ambientit/ Ministrastvo Infrastrukture i Sredine/ Ministry of Infrastructure and Environment

AGJENCIA KADASTRALE E KOSOVËS/ KOSOVSKA KATASTARSKA AGENCIJA/ KOSOVA CADASTRAL AGENCY

R E G J I S T R I M I I N DERTESËS / SHTËPISË													
Nr	Komuna	Zona Kadastrale	Numri i ndërtesës (njësia)	Etazhiteti	Katet	Sipërfaqja e kateve [m <sup>2</sup> ]	Sipërfaqja e bazamentit [m <sup>2</sup> ]	Adresa e Njësisë	Vendi i quajtur	Shfrytëzimi i aktual	Pronari / Shfrytëzuesi Emri (Emri i prindit) Mbiemri	Numri përsoneal	Pjesa e Pronës
1	Ferizaj	Ferizaj	O-72217092-_____0	B+P+1	Bodrumi	50.45	100.87	Rr. "Selim Dabinovci"- Ferizaj	KODRA E KAZERMËS	Banim	Armend (Habil) Dabinovci	1005004957	1/1
					Përdhesa	116.57							
					Kati 1	88.16							
					Gjithsej:	255.18							

Gjeodeti/kompania e licencuar: LIRIDON SEJDIU

Nr i licencës: 140

Nënshkrimi dhe vula:

















